


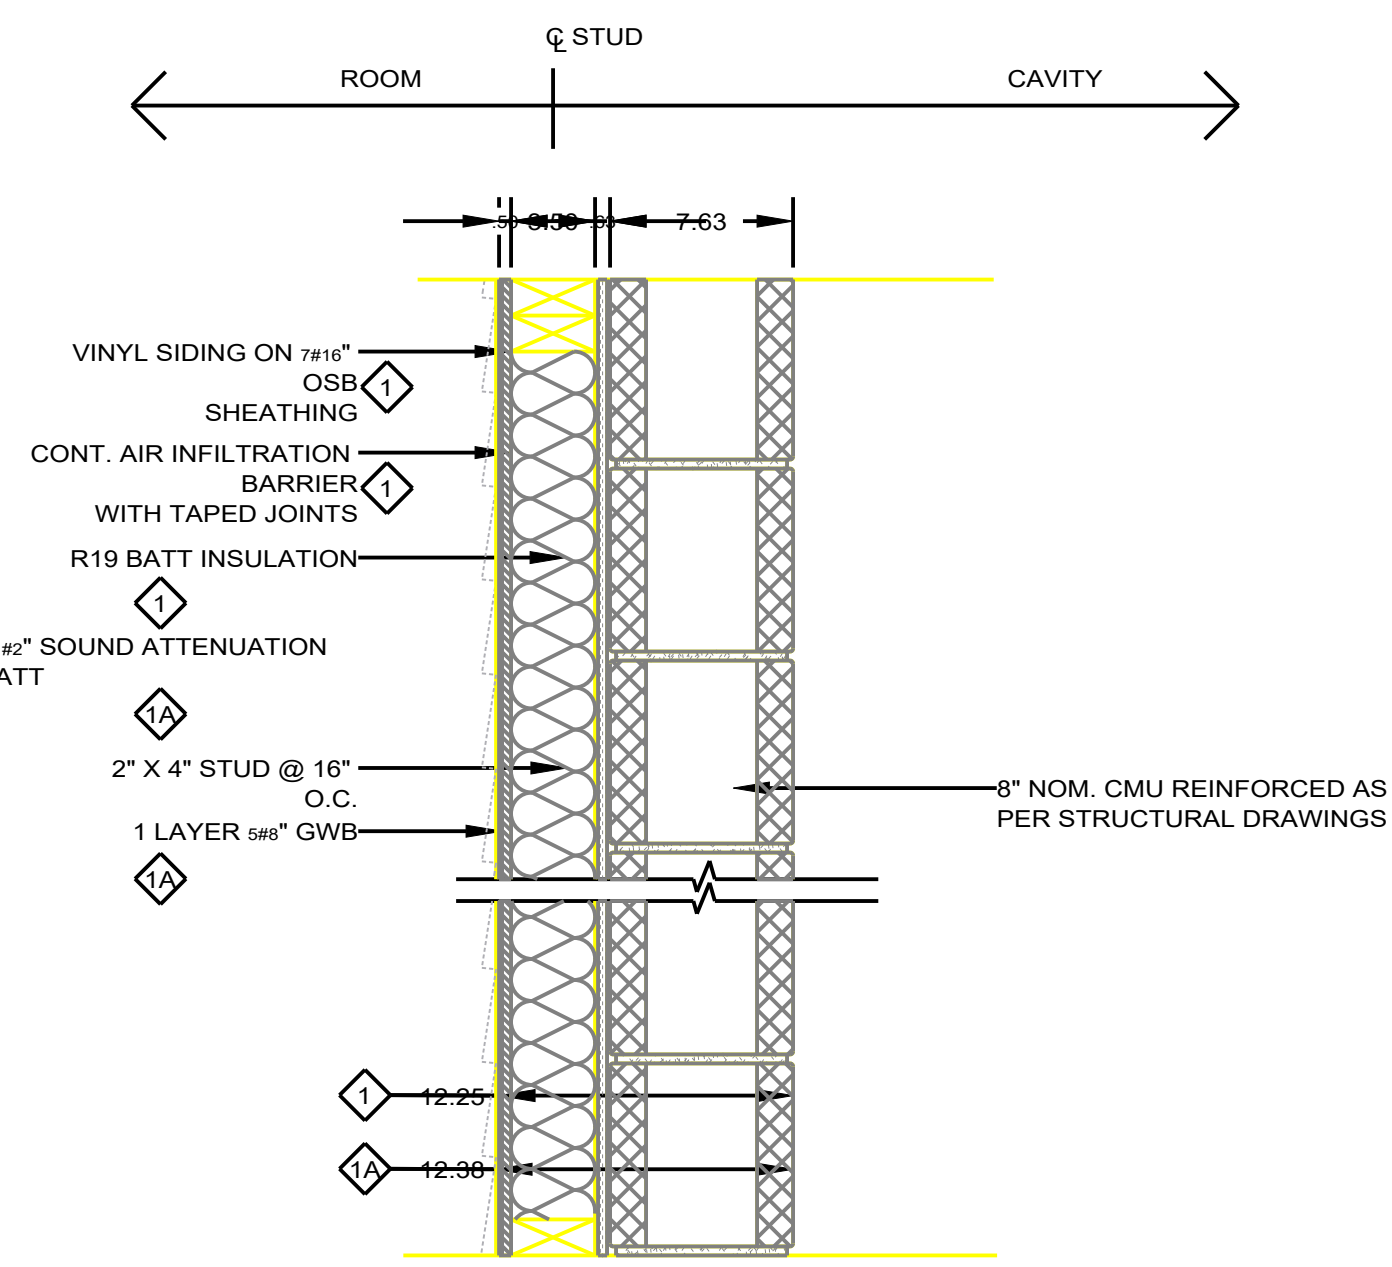


1 TWO HOUR RATED EXTERIOR BEARING FIRE

SCALE: 1/4"=1'-0"
 DESIGN NO. U306 (SIMILAR)
 VINYL SIDING, 7/16" OSB SHEATHING, 2" X 4" WOOD FRAME WITH 3/4" SOUND BATT INS., AIR INFILTRATION BARRIER WITH TAPED JOINTS, R19 BATT INSULATION, 3/4" SOUND ATTENUATION BATT, 2" X 4" STUD @ 16" O.C., 1 LAYER 5/8" GWB, 8" NOM. CMU REINFORCED AS PER STRUCTURAL DRAWINGS.

1A TWO HOUR RATED EXTERIOR BEARING FIRE

SCALE: 1/4"=1'-0"
 DESIGN NO. U306 (SIMILAR)
 1 LAYER 5/8" FIRE RATED GWB, 2" X 4" WOOD FRAME WITH 3/4" SOUND ATTENUATION BATT ON ROOM SIDE,
 1 LAYER DENSGLASS GOLD OR EQUAL, 8" NOM. CMU.

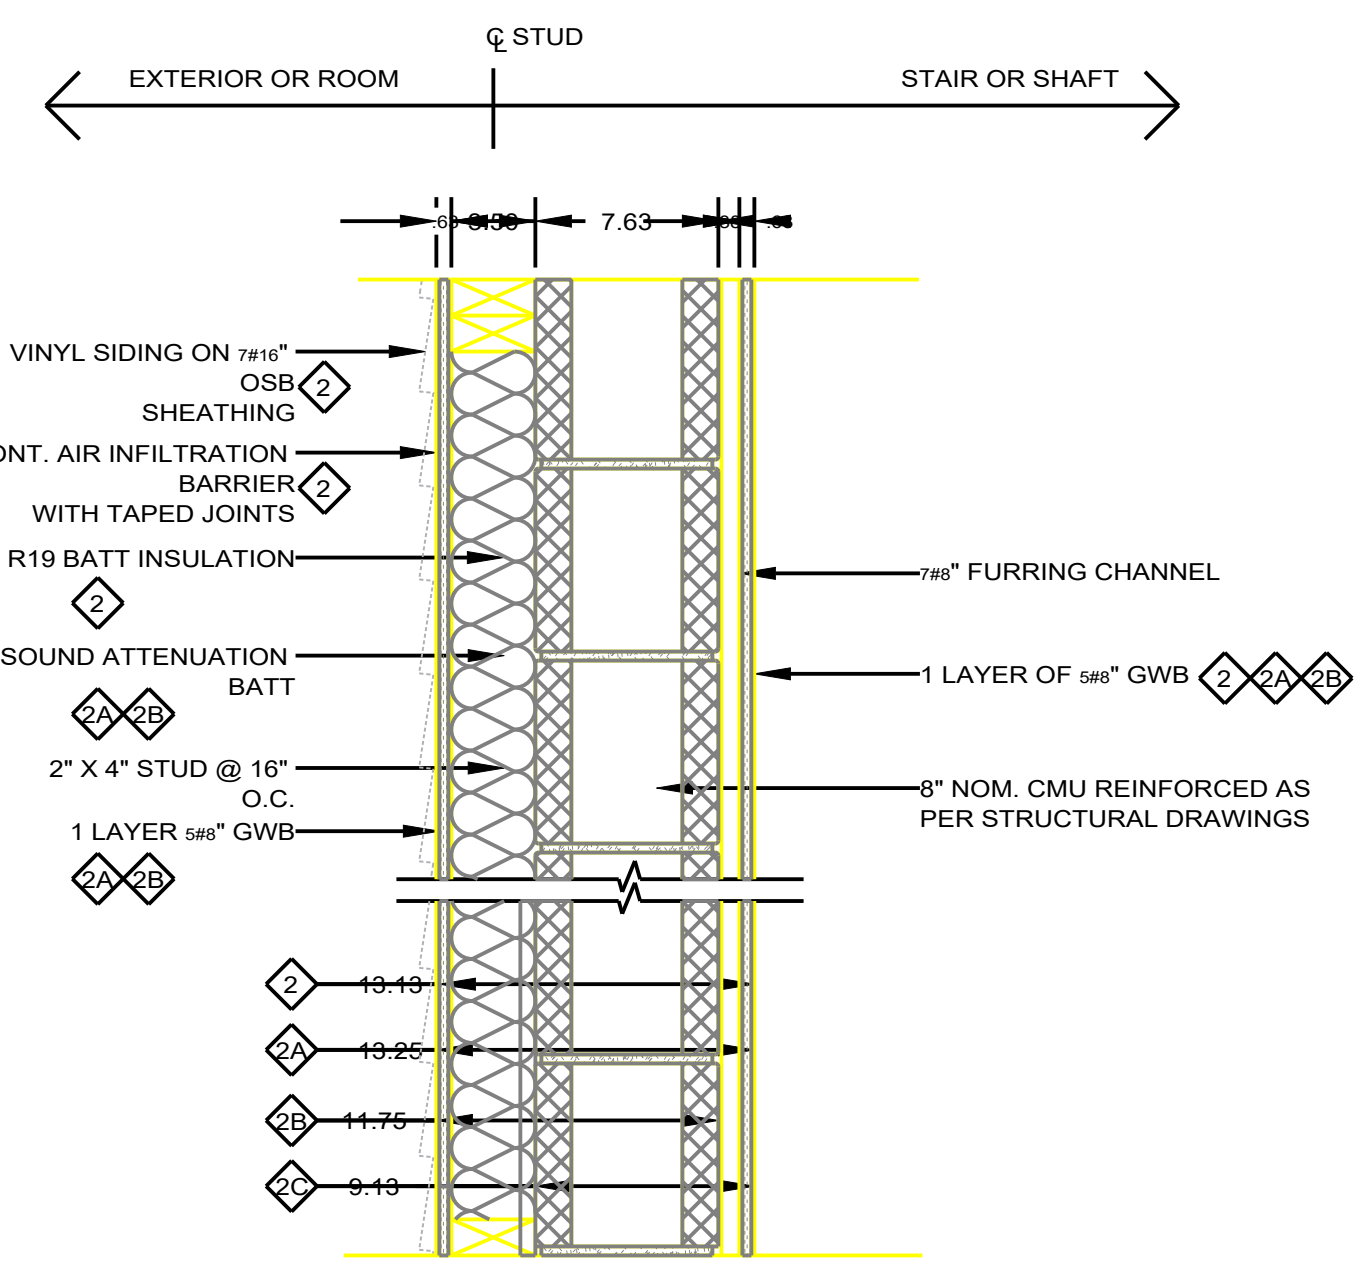

2 ONE HOUR RATED EXTERIOR MASONRY PARTITION

SCALE: 1/4"=1'-0"
 DESIGN NO. U306 (SIMILAR)
 VINYL SIDING, 7/16" OSB SHEATHING, 2" X 4" WOOD FRAME WITH 3/4" SOUND BATT INS., AIR INFILTRATION BARRIER WITH TAPED JOINTS, R19 BATT INSULATION, 3/4" SOUND ATTENUATION BATT, 2" X 4" STUD @ 16" O.C., 1 LAYER 5/8" FIRE RATED GWB ON 7/8" FURRING CHANNELS ON STAIR SIDE, 8" NOM. CMU.

2A ONE HOUR RATED EXTERIOR MASONRY PARTITION


SCALE: 1/4"=1'-0"
 DESIGN NO. U306 (SIMILAR)
 1 LAYER 5/8" FIRE RATED GWB ON 2" X 4" WOOD FRAME WITH 3/4" SOUND ATTENUATION BATT ON ROOM SIDE, 8" NOM. CMU, NO FURRING OR GWB ON SHAFT SIDE.

2B ONE HOUR RATED EXTERIOR MASONRY PARTITION

SCALE: 1/4"=1'-0"
 DESIGN NO. U306 (SIMILAR)
 1 LAYER 5/8" FIRE RATED GWB ON 2" X 4" WOOD FRAME WITH 3/4" SOUND ATTENUATION BATT ON ROOM SIDE, 8" NOM. CMU, NO FURRING OR GWB ON SHAFT SIDE.

2C ONE HOUR RATED INTERIOR MASONRY PARTITION

SCALE: 1/4"=1'-0"
 DESIGN NO. U306 (SIMILAR)
 NO GWB, WOOD FRAME OR SOUND ATTENUATION BATT ON ROOM SIDE, 8" NOM. CMU, 1 LAYER 5/8" FIRE RATED GWB ON 7/8" FURRING CHANNELS ON STAIR SIDE.

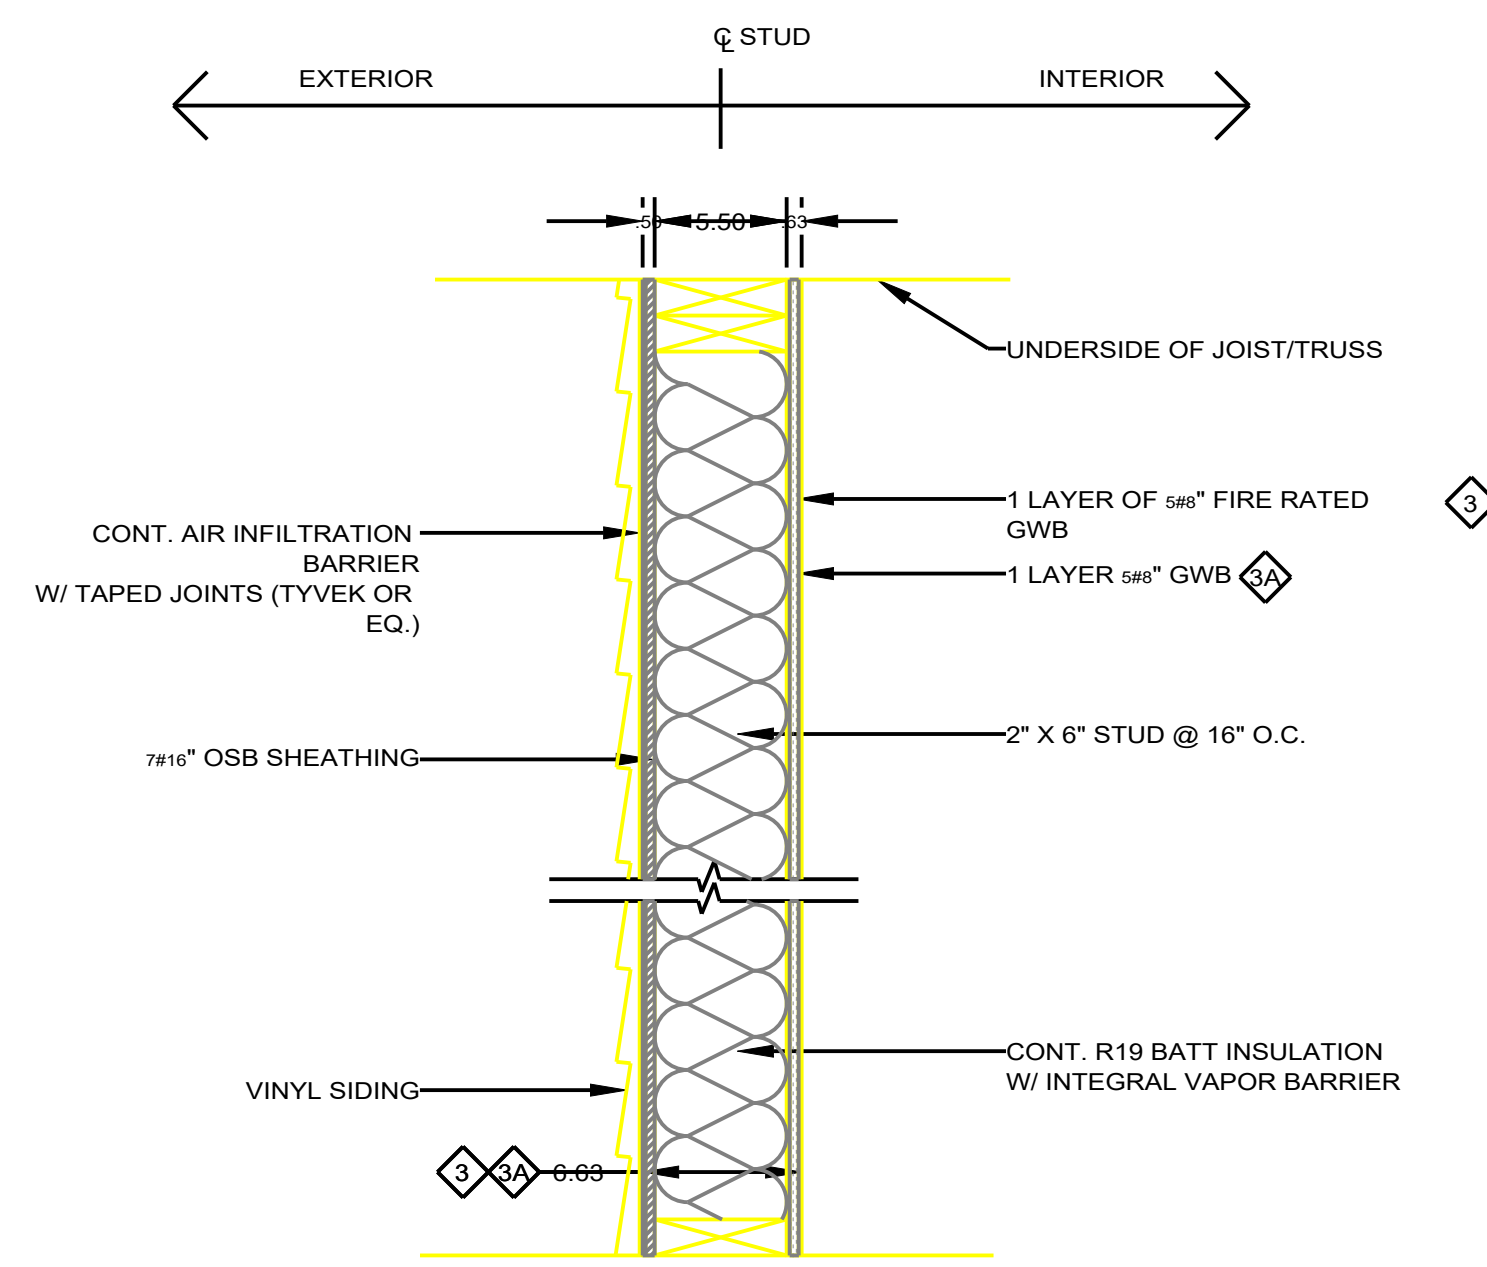


3 ONE HOUR RATED EXTERIOR BEARING PARTITION

SCALE: 1/4"=1'-0"
 DESIGN NO. U306
 VINYL SIDING, 1 LAYER 7/16" OSB SHEATHING WITH AIR INFILTRATION BARRIER ON EXTERIOR SIDE, 2" X 6" WOOD FRAME WITH R19 BATT INSULATION, 1 LAYER 5/8" FIRE RATED GWB ON INTERIOR SIDE.

3A NON-RATED EXTERIOR BEARING PARTITION

SCALE: 1/4"=1'-0"
 DESIGN NO. U305 (SIMILAR)
 VINYL SIDING, 1 LAYER 7/16" OSB SHEATHING WITH AIR INFILTRATION BARRIER ON EXTERIOR SIDE, 2" X 6" WOOD FRAME WITH R19 BATT INSULATION, 1 LAYER 5/8" GWB ON INTERIOR SIDE.

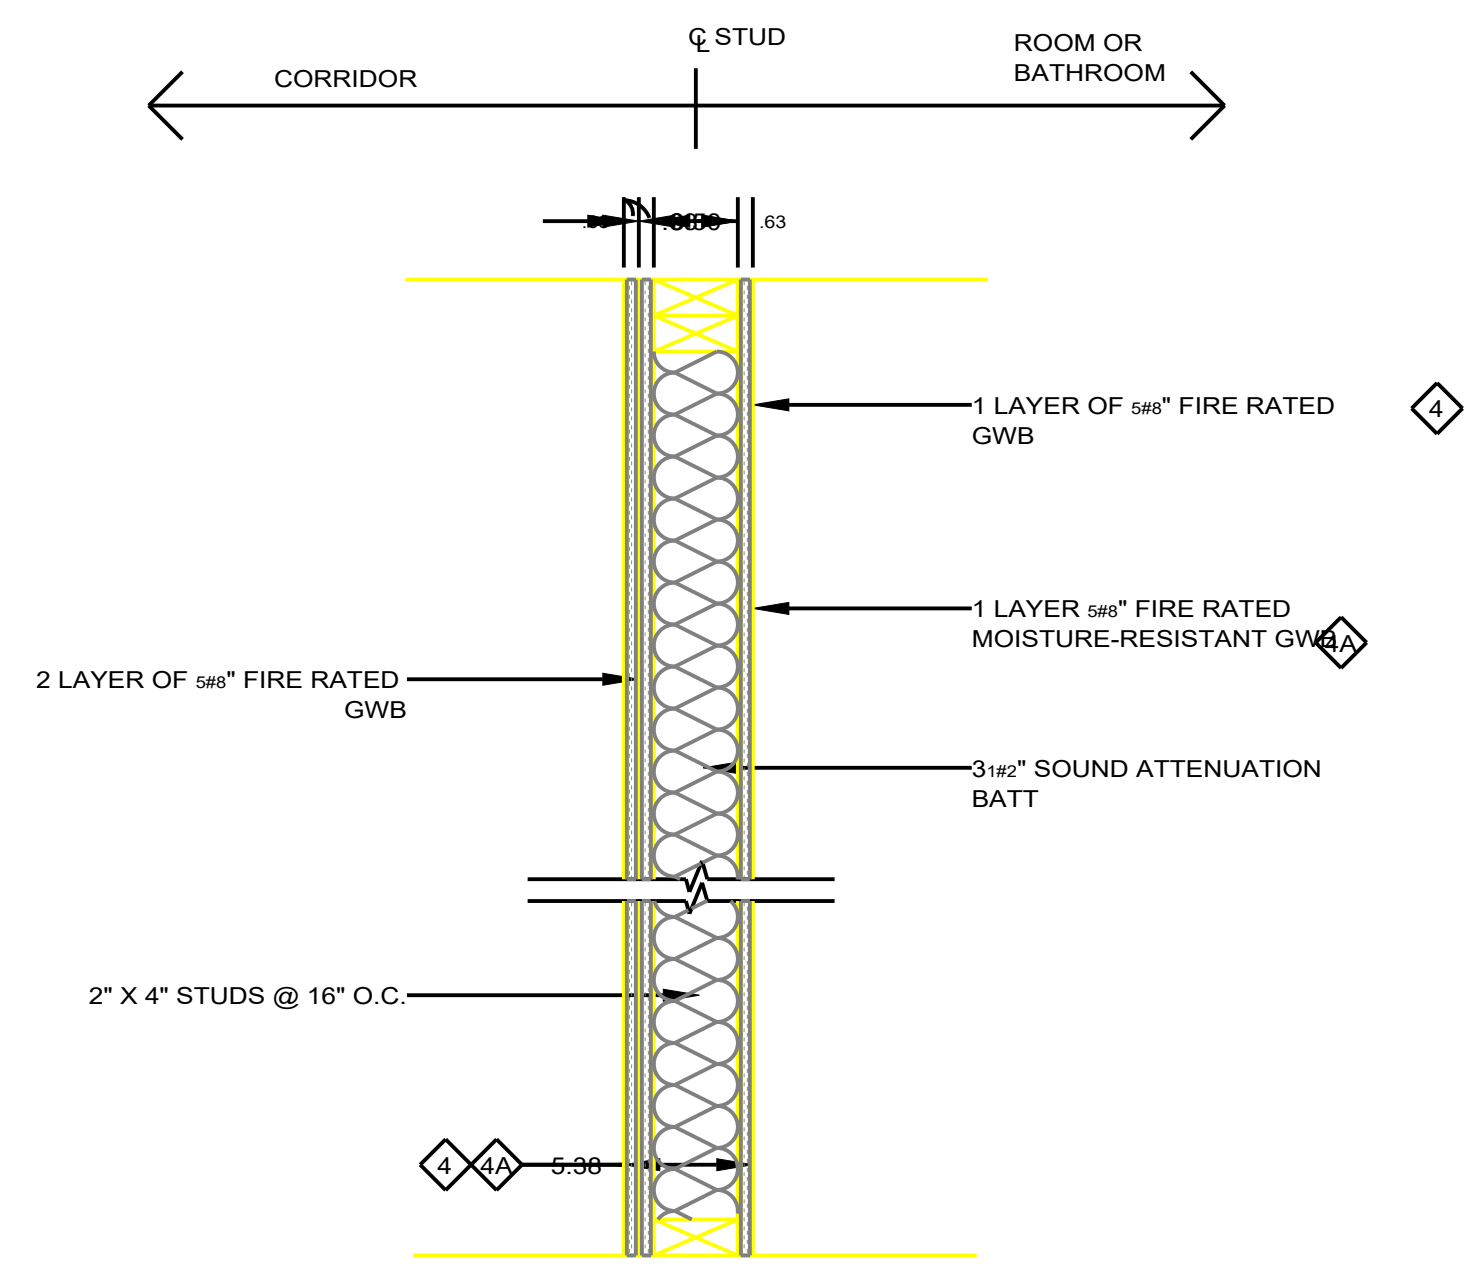


4 ONE HR RATED INTERIOR BEARING PARTITION

SCALE: 1/4"=1'-0"
 DESIGN NO. U305 (SIMILAR)
 2 LAYER 5/8" FIRE RATED GWB ON CORRIDOR SIDE, 2" X 4" WOOD FRAME WITH 3/4" SOUND ATTENUATION BATT, 1 LAYER 5/8" FIRE RATED GWB ON ROOM SIDE.

4A ONE HR RATED INTERIOR BEARING PARTITION

SCALE: 1/4"=1'-0"
 DESIGN NO. U305 (SIMILAR)
 2 LAYER 5/8" FIRE RATED GWB ON CORRIDOR SIDE, 2" X 4" WOOD FRAME WITH 3/4" SOUND ATTENUATION BATT, 1 LAYER 5/8" FIRE RATED MOISTURE-RESISTANT GWB ON BATHROOM SIDE.

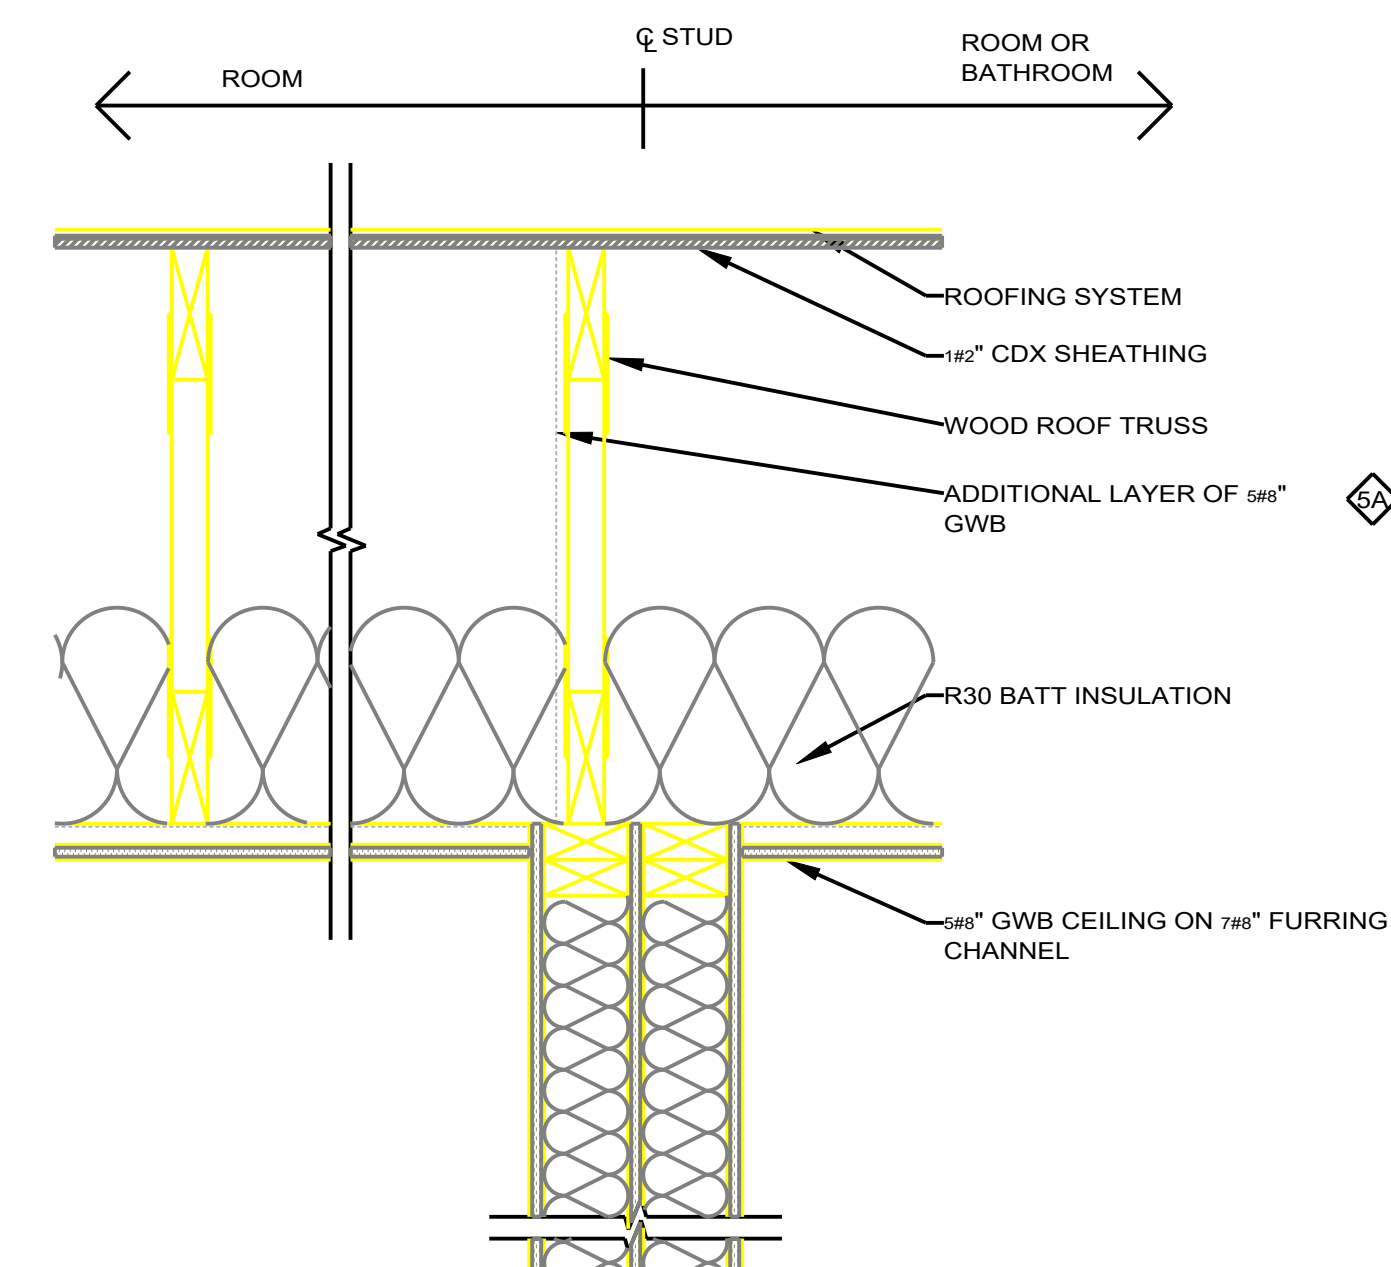

5 ONE HOUR RATED INTERIOR DEMISING PARTITION

SCALE: 1/4"=1'-0"
 WALL DESIGN NO. U305 (SIMILAR), FLOOR DESIGN NO. L521, ROOF DESIGN NO. P531
 1 LAYER 5/8" FIRE RATED GWB, 2" X 4" WOOD FRAME WITH 3/4" SOUND ATTENUATION BATT ON ROOM SIDE,
 1 LAYER 5/8" DENSGLASS GOLD OR EQUAL,
 1 LAYER 5/8" FIRE RATED GWB, 2" X 4" WOOD FRAME WITH 3/4" SOUND ATTENUATION BATT ON OTHER SIDE.

5A ONE HOUR RATED INTERIOR DEMISING PARTITION


SCALE: 1/4"=1'-0"
 WALL DESIGN NO. U305 (SIMILAR), FLOOR DESIGN NO. L521, ROOF DESIGN NO. P531
 1 LAYER 5/8" FIRE RATED GWB, 2" X 4" WOOD FRAME WITH 3/4" SOUND ATTENUATION BATT ON ROOM SIDE,
 1 LAYER 5/8" DENSGLASS GOLD OR EQUAL,
 1 LAYER 5/8" FIRE RATED GWB, 2" X 4" WOOD FRAME WITH 3/4" SOUND ATTENUATION BATT ON OTHER SIDE.

5B ONE HOUR RATED INTERIOR DEMISING PARTITION

SCALE: 1/4"=1'-0"
 WALL DESIGN NO. U305 (SIMILAR), FLOOR DESIGN NO. L521, ROOF DESIGN NO. P531
 1 LAYER 5/8" FIRE RATED GWB, 2" X 4" WOOD FRAME WITH 3/4" SOUND ATTENUATION BATT ON ROOM SIDE,
 1 LAYER 5/8" FIRE RATED MOISTURE-RESISTANT GWB, 2" X 4" WOOD FRAME WITH 3/4" SOUND ATTENUATION BATT, 1 LAYER 5/8" FIRE RATED MOISTURE-RESISTANT GWB TO COVER EDGE OF TUB.

5C ONE HOUR RATED INTERIOR DEMISING PARTITION

SCALE: 1/4"=1'-0"
 WALL DESIGN NO. U305 (SIMILAR), FLOOR DESIGN NO. L521, ROOF DESIGN NO. P531
 1 LAYER 5/8" FIRE RATED GWB, 2" X 4" WOOD FRAME WITH 3/4" SOUND ATTENUATION BATT ON ROOM SIDE,
 1 LAYER 5/8" DENSGLASS GOLD OR EQUAL,
 1 LAYER 5/8" FIRE RATED MOISTURE-RESISTANT GWB, 2" X 4" WOOD FRAME WITH 3/4" SOUND ATTENUATION BATT, 1 LAYER 5/8" FIRE RATED MOISTURE-RESISTANT GWB TO COVER EDGE OF TUB.

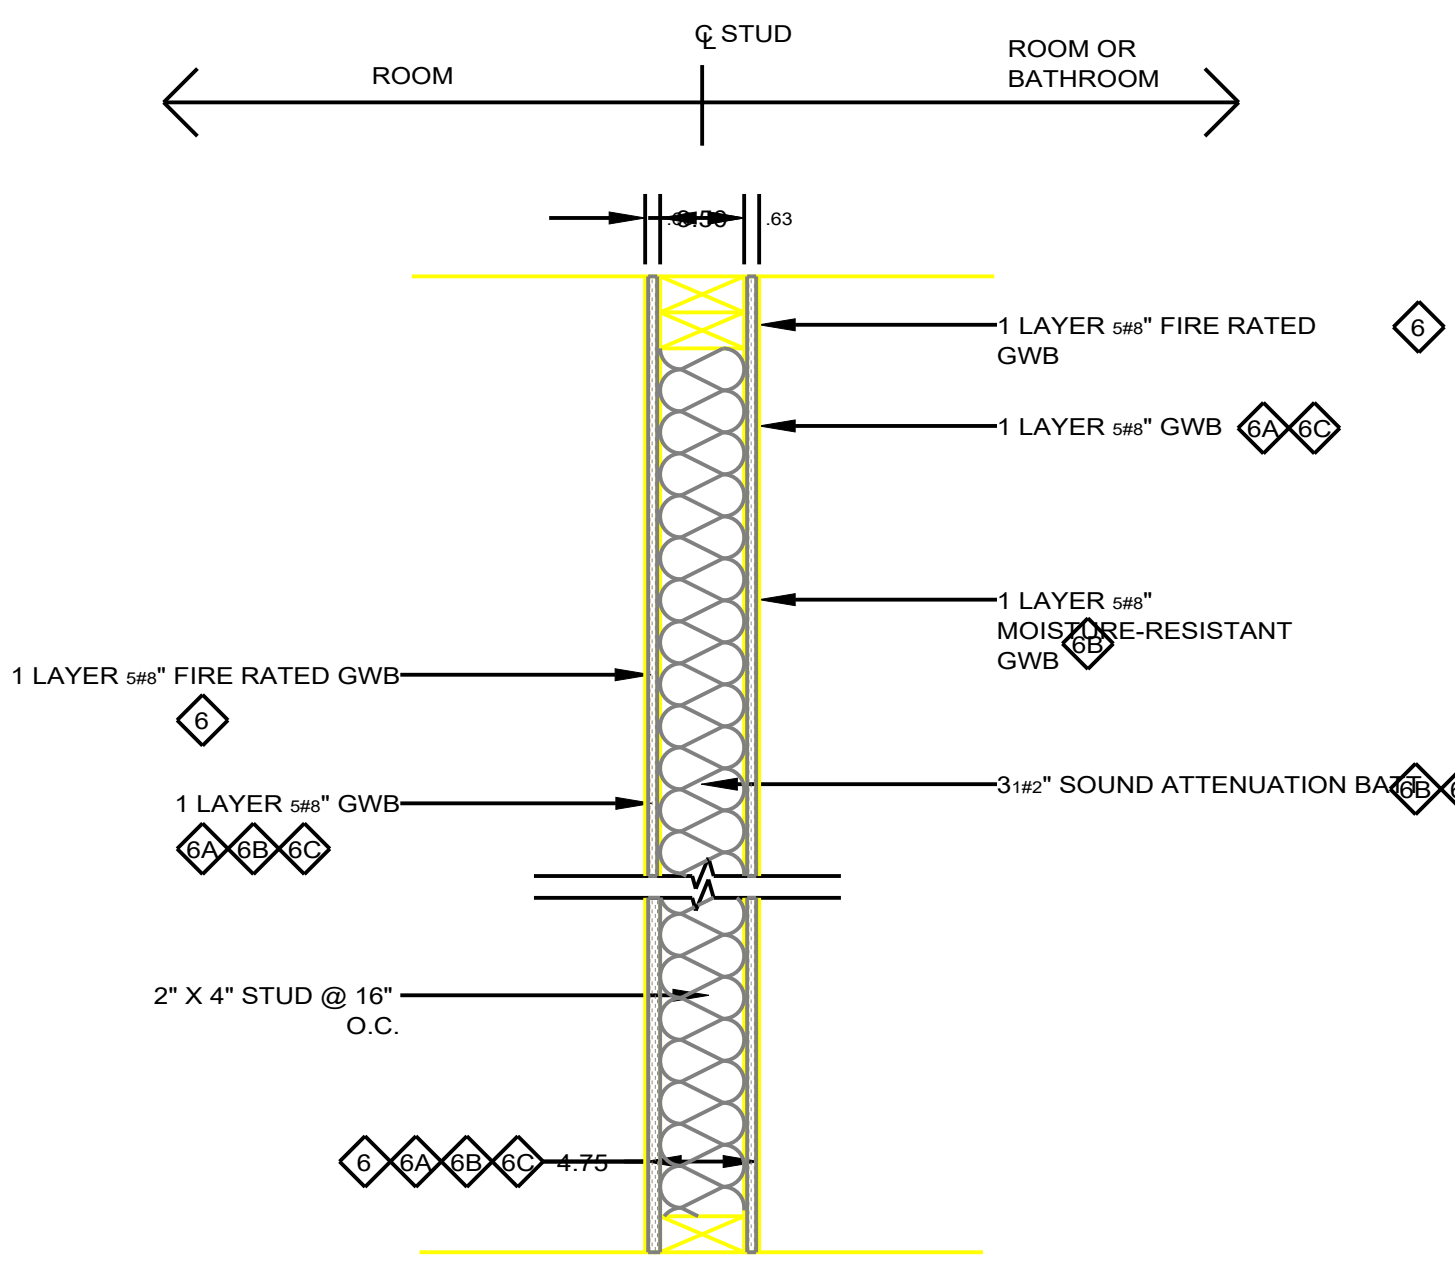

6 ONE HR RATED INTERIOR BEARING PARTITION

SCALE: 1/4"=1'-0"
 DESIGN NO. U305
 1 LAYER 5/8" FIRE RATED GWB ON EACH SIDE, 2" X 4" WOOD FRAME WITH 3/4" SOUND ATTENUATION BATT.

6A NON-RATED INTERIOR PARTITION


SCALE: 1/4"=1'-0"
 1 LAYER 5/8" GWB ON EACH SIDE, 2" X 4" WOOD FRAME.

6B NON-RATED INTERIOR PARTITION

SCALE: 1/4"=1'-0"
 MIN. STC RATING: 36
 1 LAYER 5/8" GWB ON ROOM SIDE, 2" X 4" WOOD FRAME WITH 3/4" SOUND ATTENUATION BATT, 1 LAYER 5/8" MOISTURE-RESISTANT GWB ON BATHROOM SIDE.

6C NON-RATED INTERIOR PARTITION

SCALE: 1/4"=1'-0"
 MIN. STC RATING: 36
 1 LAYER 5/8" GWB ON EACH SIDE, 2" X 4" WOOD FRAME WITH 3/4" SOUND ATTENUATION BATT.

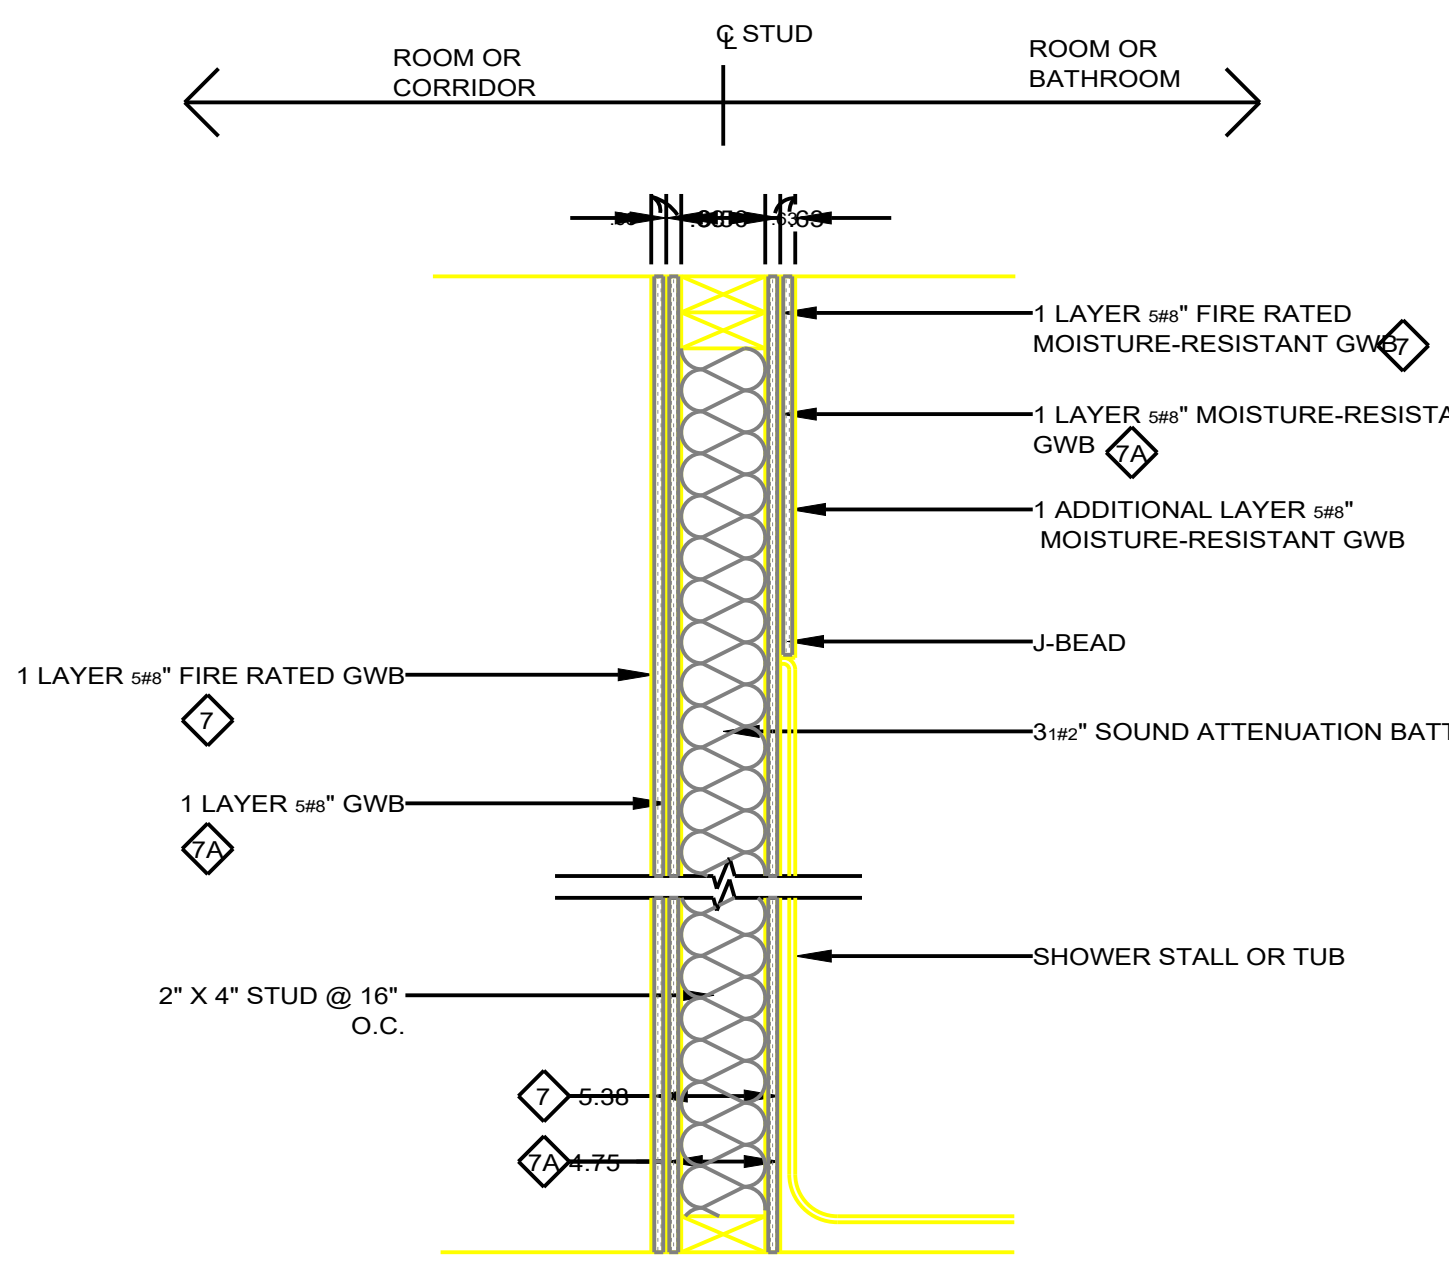


7 ONE HR RATED INTERIOR BEARING PARTITION

SCALE: 1/4"=1'-0"
 DESIGN NO. U305 (SIMILAR)
 2 LAYERS 5/8" FIRE RATED GWB ON CORRIDOR SIDE, 2" X 4" WOOD FRAME WITH 3/4" SOUND ATTENUATION BATT, 1 LAYER 5/8" FIRE RATED MOISTURE-RESISTANT GWB ON BATHROOM SIDE, 1 ADDITIONAL LAYER 5/8" MOISTURE-RESISTANT GWB TO COVER EDGE OF TUB.

7A NON-RATED INTERIOR PARTITION

SCALE: 1/4"=1'-0"
 MIN. STC RATING: 50
 1 LAYER 5/8" GWB ON ROOM SIDE, 2" X 4" WOOD FRAME WITH 3/4" SOUND ATTENUATION BATT, 1 LAYER 5/8" MOISTURE-RESISTANT GWB ON BATHROOM SIDE, 1 ADDITIONAL LAYER 5/8" MOISTURE-RESISTANT GWB TO COVER EDGE OF TUB.

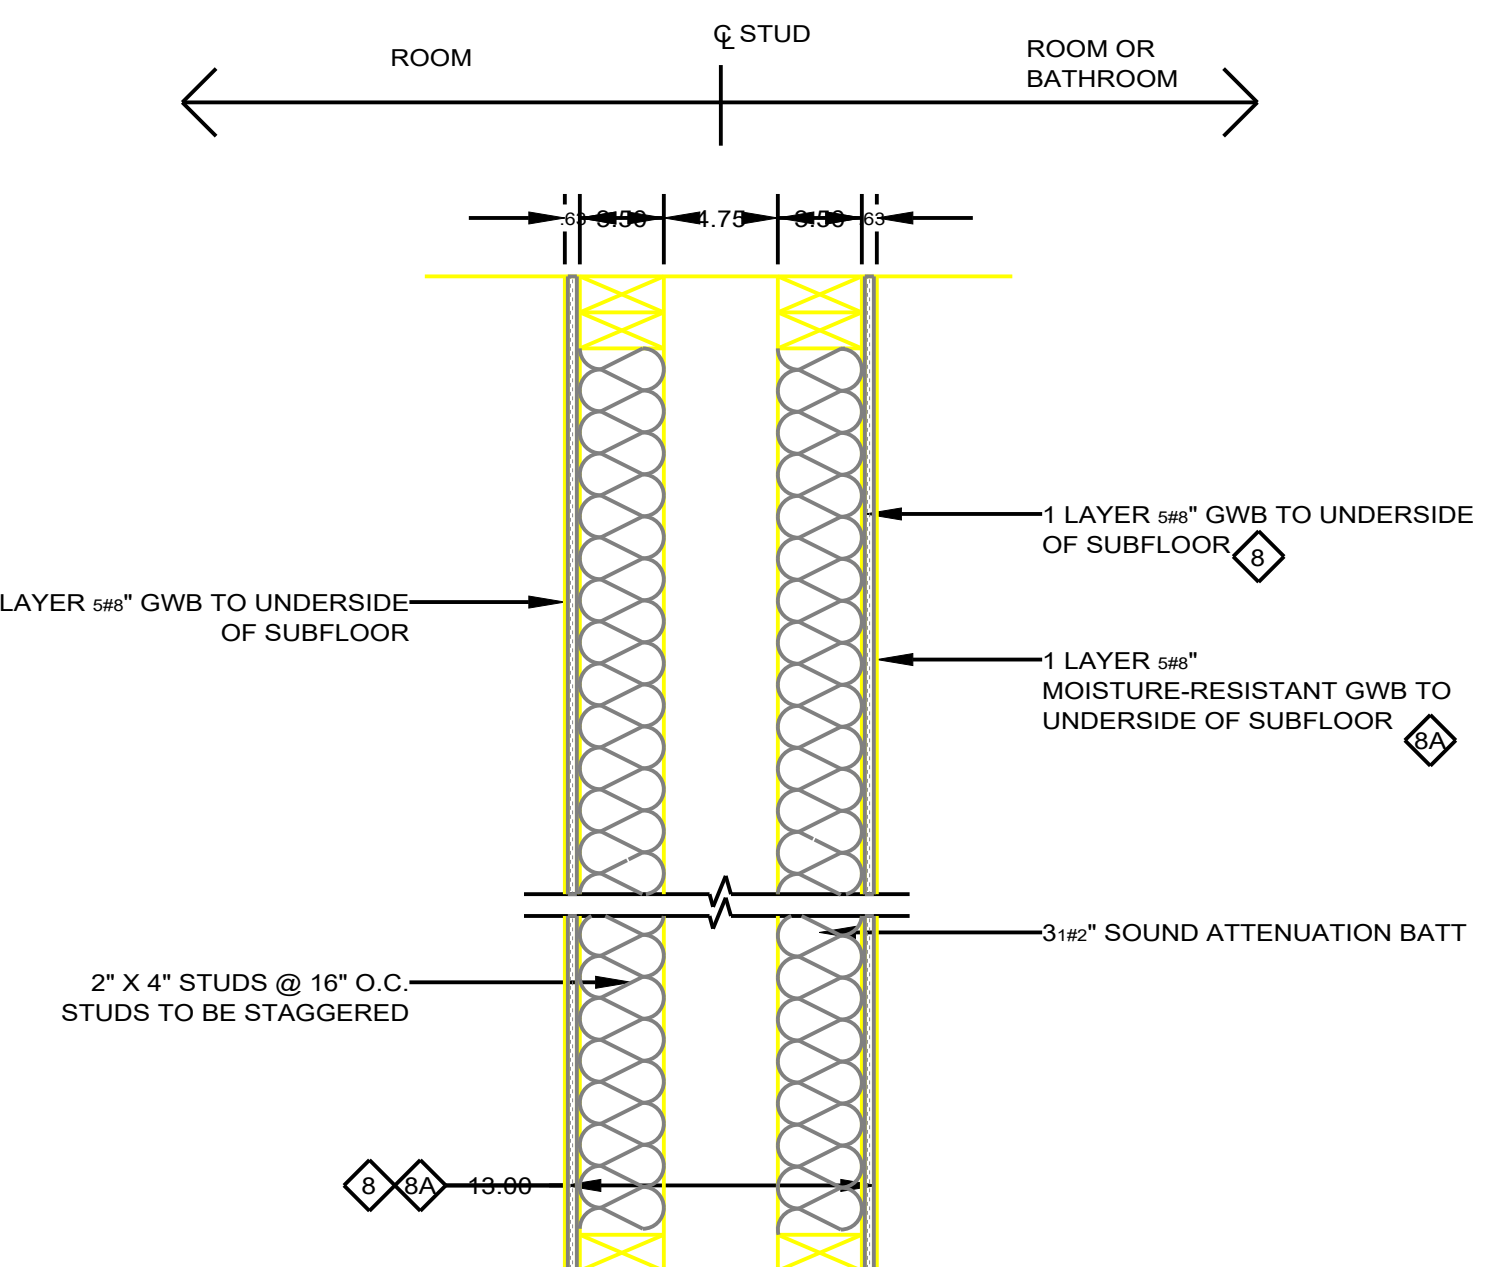


8 NON-RATED PLUMBING CHASE

SCALE: 1/4"=1'-0"
 MIN. STC RATING: 46
 1 LAYER 5/8" GWB, 2" X 4" WOOD FRAME WITH 3/4" SOUND ATTENUATION BATT ON ROOM SIDE, 1 LAYER 5/8" GWB, 2" X 4" WOOD FRAME WITH 3/4" SOUND ATTENUATION BATT ON OTHER SIDE.

8A NON-RATED PLUMBING CHASE

SCALE: 1/4"=1'-0"
 1 LAYER 5/8" GWB, 2" X 4" WOOD FRAME WITH 3/4" SOUND ATTENUATION BATT ON ROOM SIDE, 1 LAYER 5/8" MOISTURE-RESISTANT GWB, 2" X 4" WOOD FRAME WITH 3/4" SOUND ATTENUATION BATT ON BATHROOM SIDE.

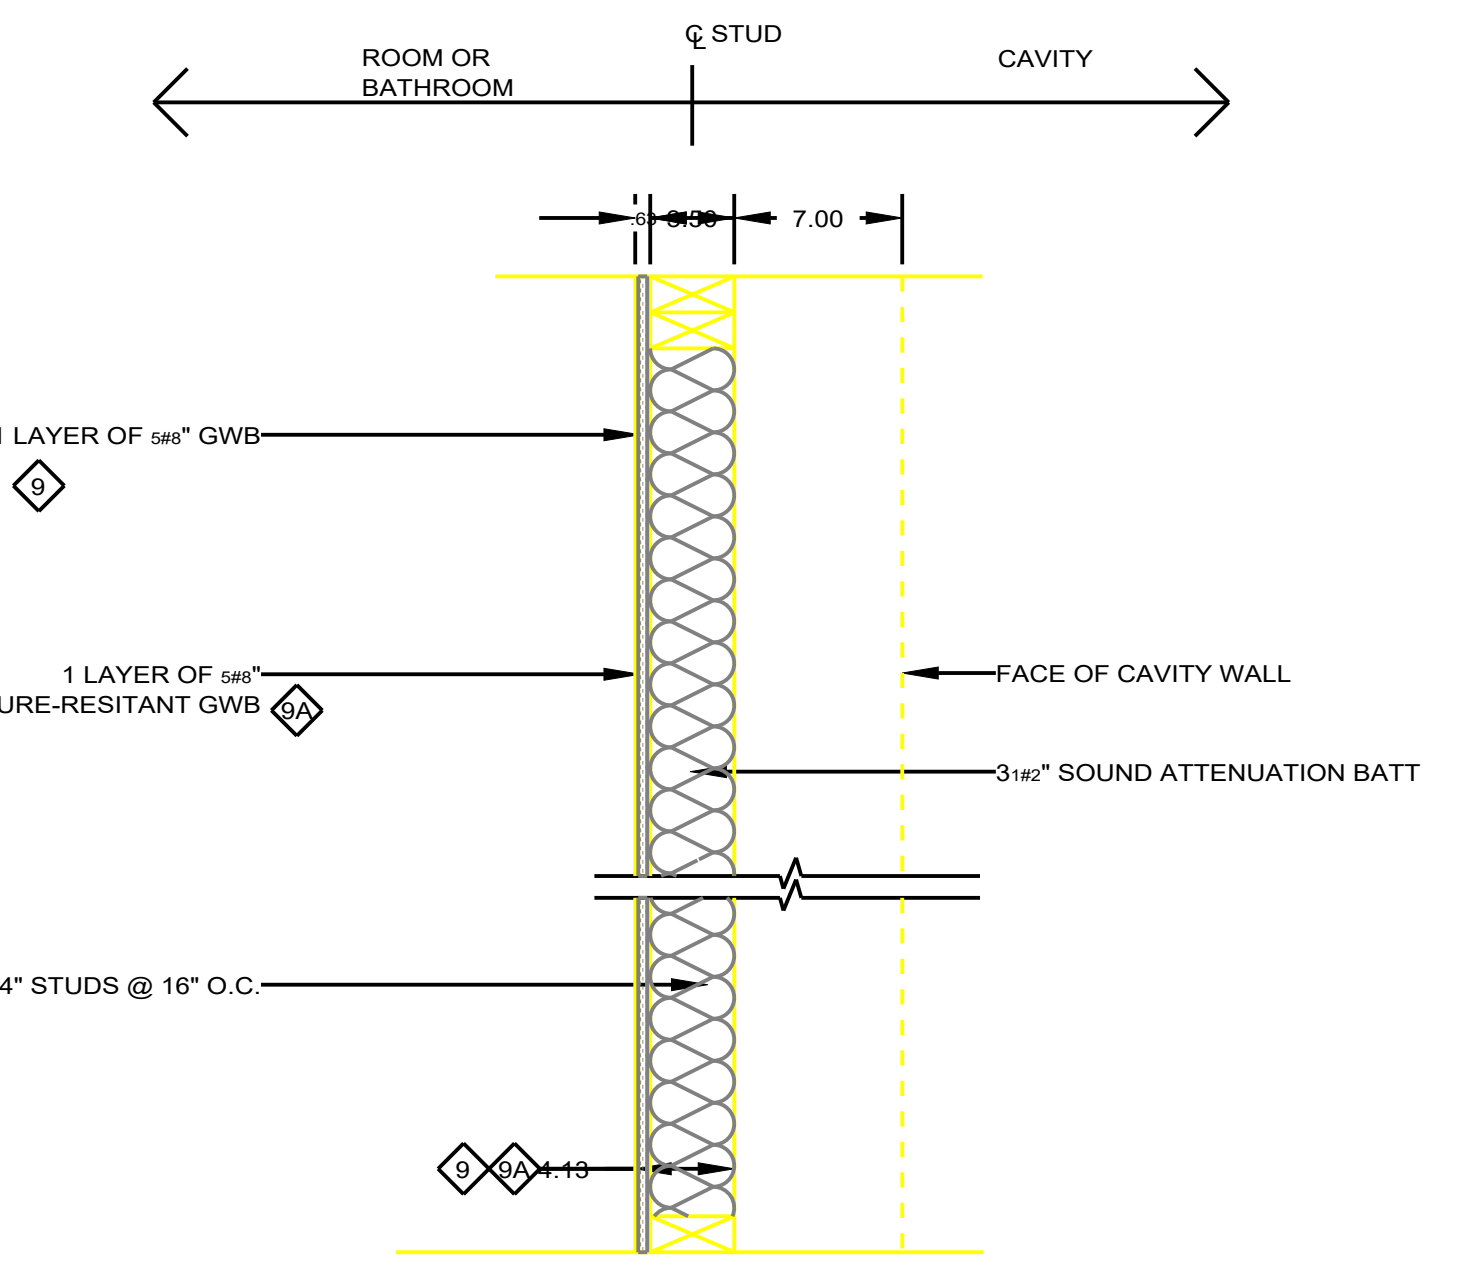


9 NON-RATED INTERIOR FURRING

SCALE: 1/4"=1'-0"
 1 LAYER 5/8" GWB ON ROOM SIDE, 2" X 4" WOOD FRAME WITH 3/4" SOUND ATTENUATION BATT.

9A NON-RATED INTERIOR FURRING

SCALE: 1/4"=1'-0"
 1 LAYER 5/8" MOISTURE-RESISTANT GWB ON BATHROOM SIDE, 2" X 4" WOOD FRAME WITH 3/4" SOUND ATTENUATION BATT.

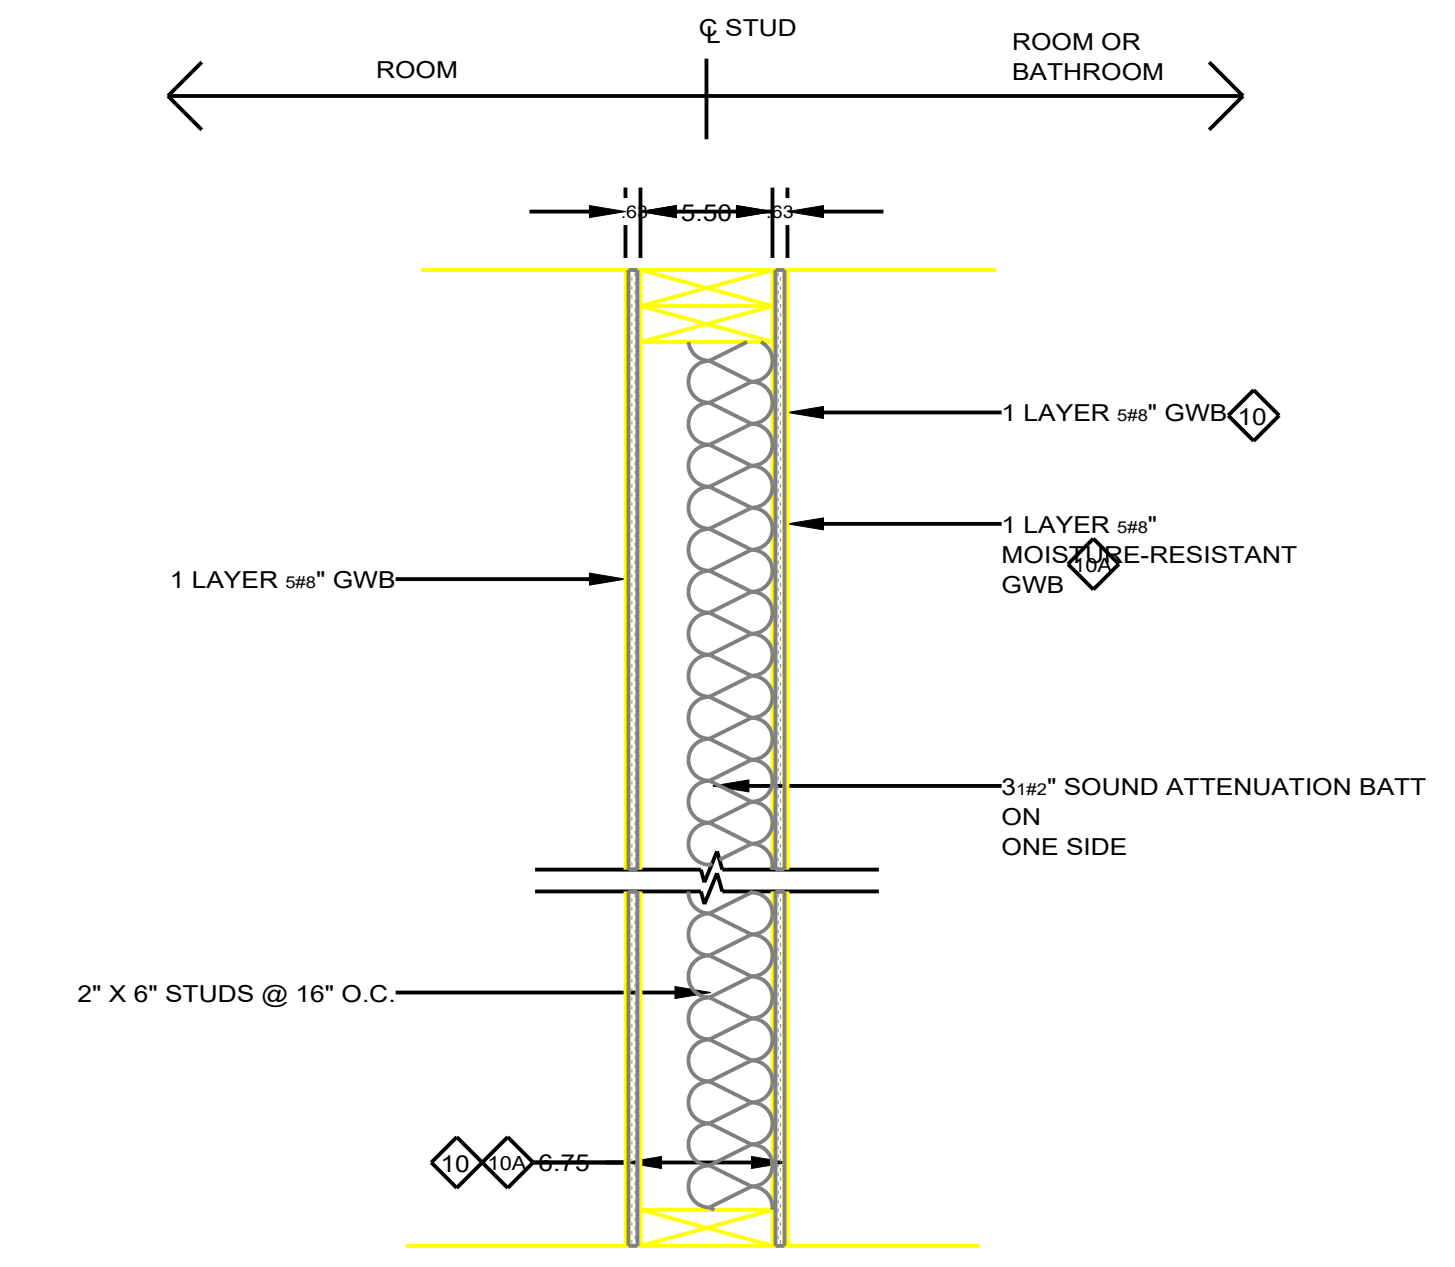


10 NON-RATED INTERIOR PARTITION

SCALE: 1/4"=1'-0"
 MIN. STC RATING: 36
 1 LAYER 5/8" GWB ON EACH SIDE, 2" X 6" WOOD FRAME WITH 5/8" SOUND ATTENUATION BATT.


10A NON-RATED INTERIOR PARTITION

SCALE: 1/4"=1'-0"
 MIN. STC RATING: 36
 1 LAYER 5/8" GWB ON ROOM SIDE, 2" X 6" WOOD FRAME WITH 5/8" SOUND ATTENUATION BATT, 1 LAYER 5/8" MOISTURE-RESISTANT GWB ON BATHROOM SIDE.

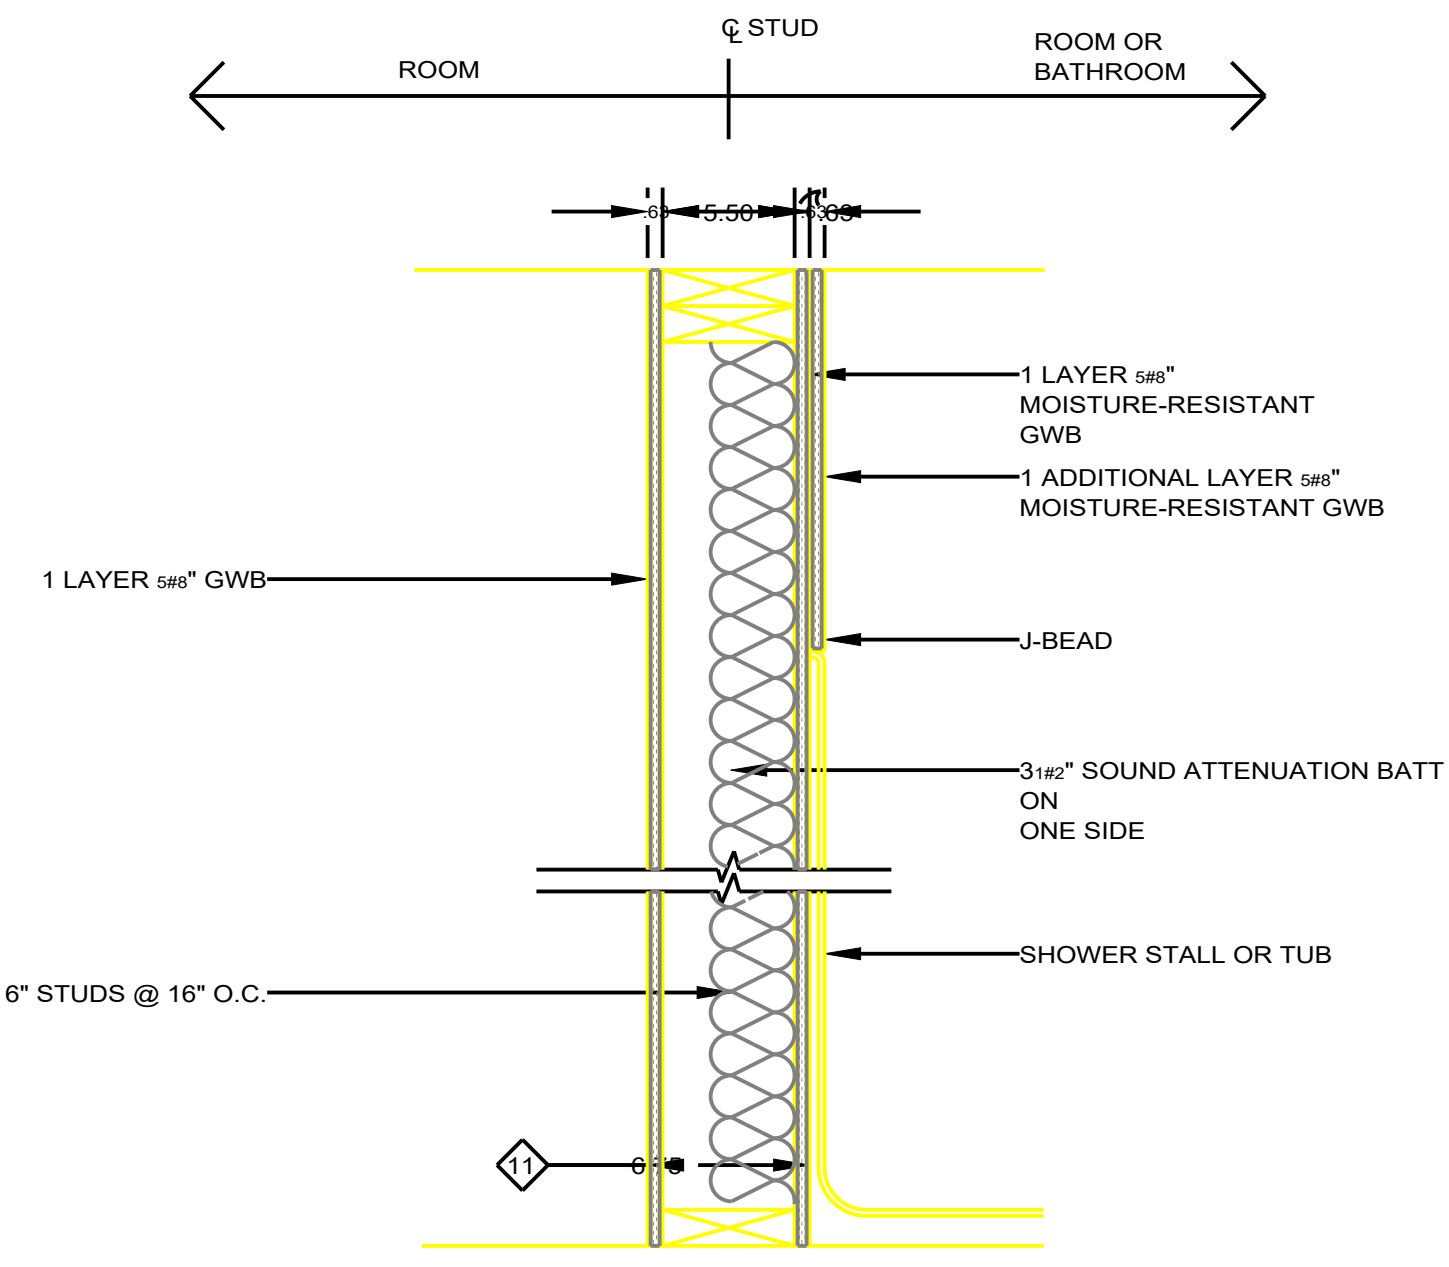


11 NON-RATED INTERIOR PARTITION

SCALE: 1/4"=1'-0"
 MIN. STC RATING: 36
 1 LAYER 5/8" GWB ON ROOM SIDE, 2" X 6" WOOD FRAME WITH 5/8" SOUND ATTENUATION BATT, 1 LAYER 5/8" MOISTURE-RESISTANT GWB TO COVER EDGE OF TUB, 1 ADDITIONAL LAYER 5/8" MOISTURE-RESISTANT GWB TO COVER EDGE OF TUB.

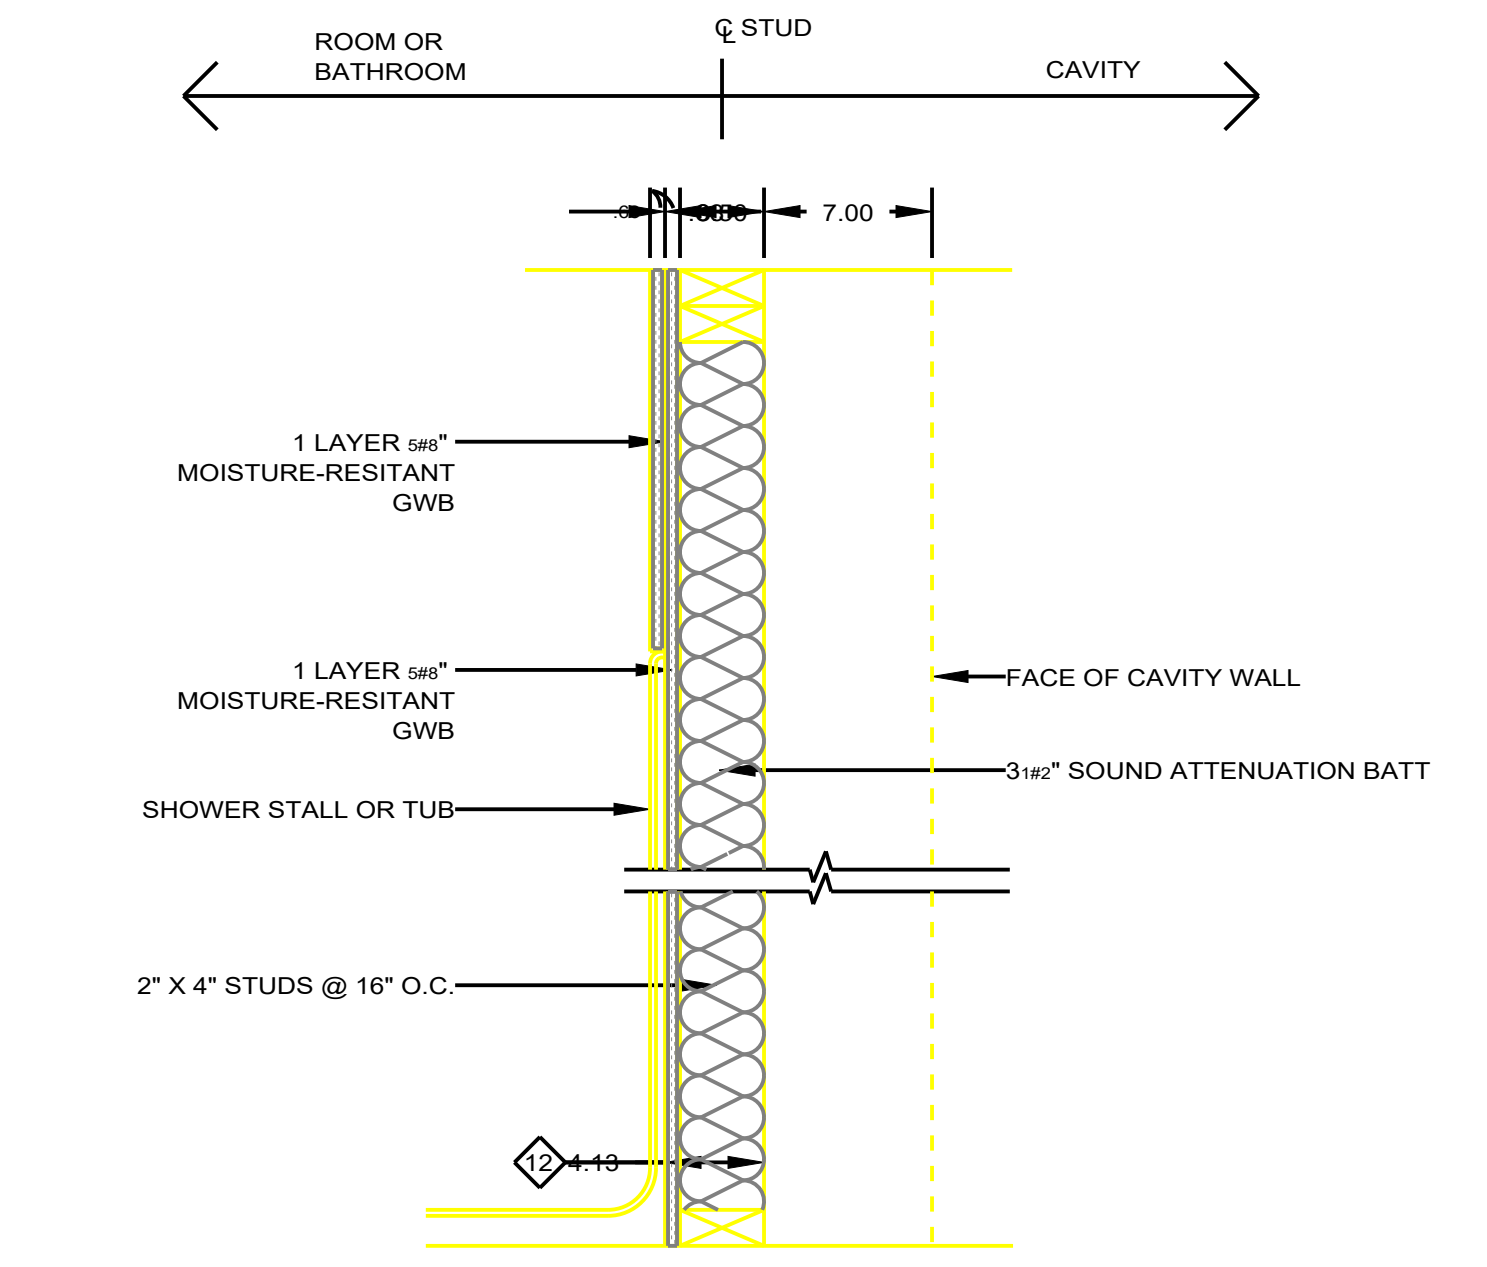

12 NON-RATED INTERIOR FURRING

SCALE: 1/4"=1'-0"
 1 LAYER 5/8" MOISTURE-RESISTANT GWB ON BATHROOM SIDE, 1 ADDITIONAL LAYER 5/8" MOISTURE-RESISTANT GWB TO COVER EDGE OF TUB, 2" X 4" WOOD FRAME WITH 3/4" SOUND ATTENUATION BATT.

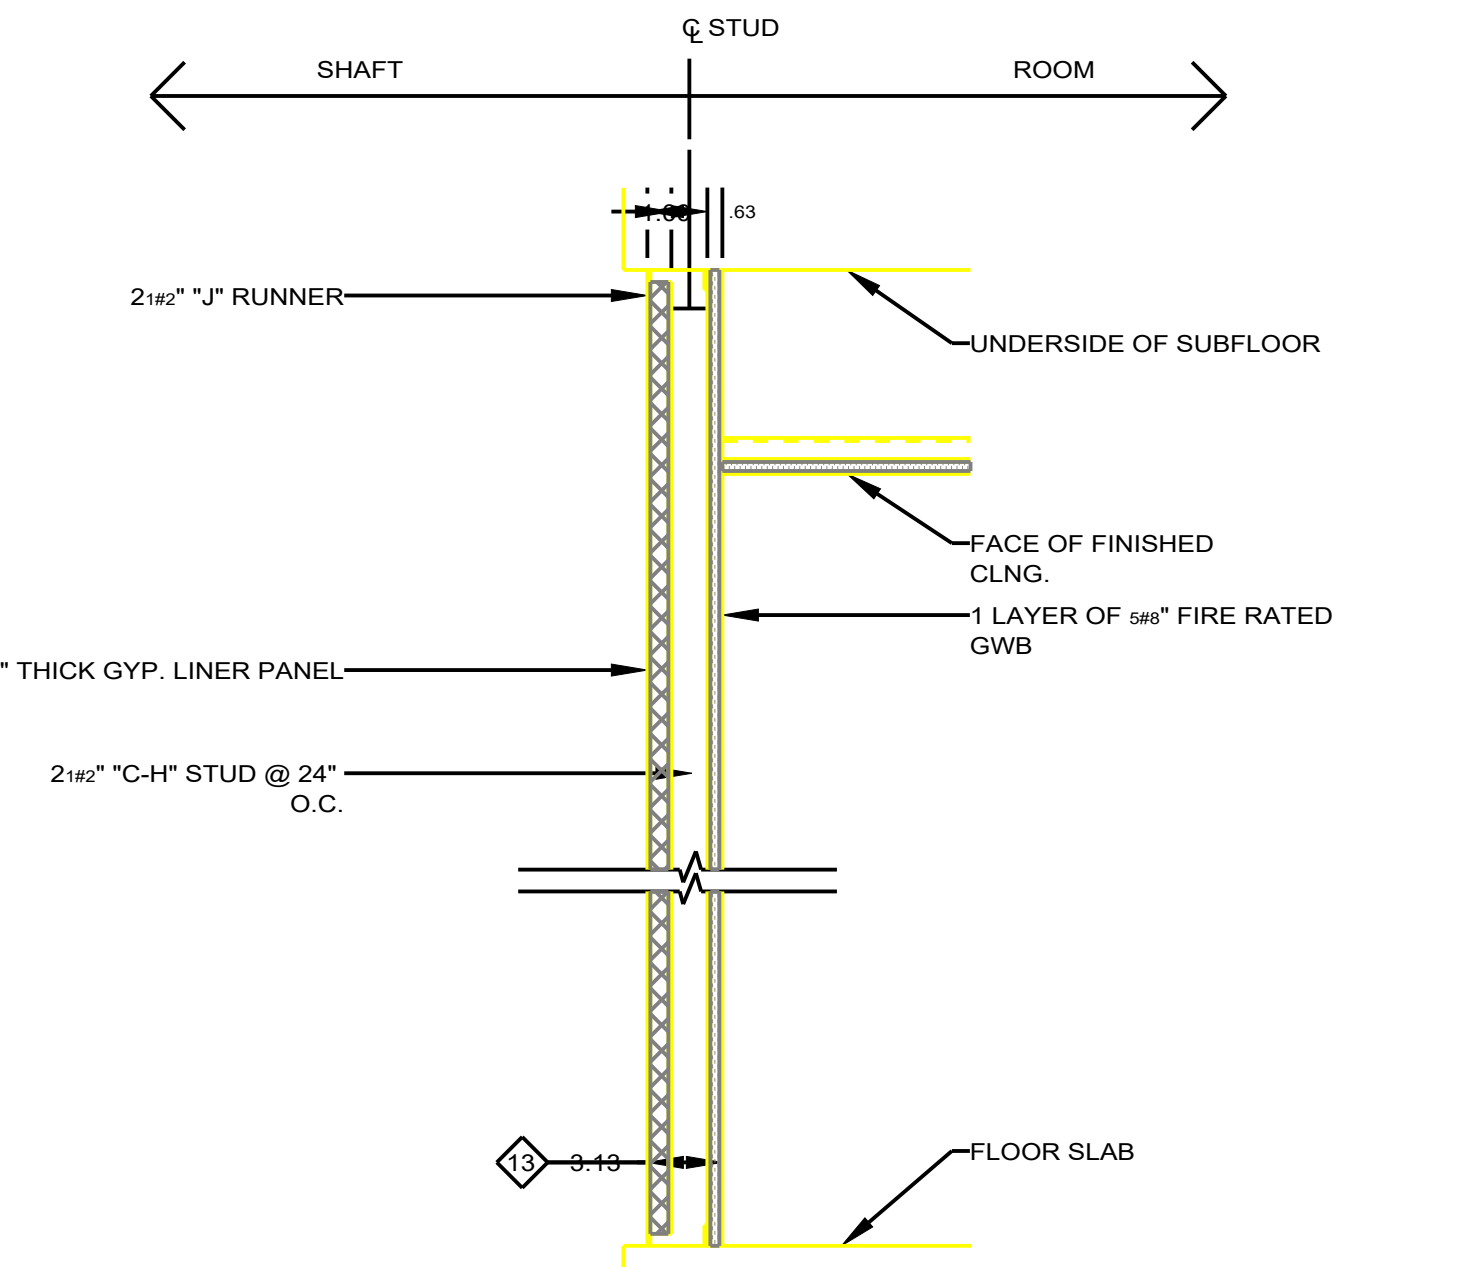

13 ONE HR RATED SHAFT WALL

SCALE: 1/4"=1'-0"
 DESIGN NO. L469
 1" THICK GYP LINER PANEL ON SHAFT SIDE, 2" X 4" WOOD FRAME WITH 3/4" SOUND ATTENUATION BATT, 1 LAYER 5/8" GWB ON ROOM SIDE.