



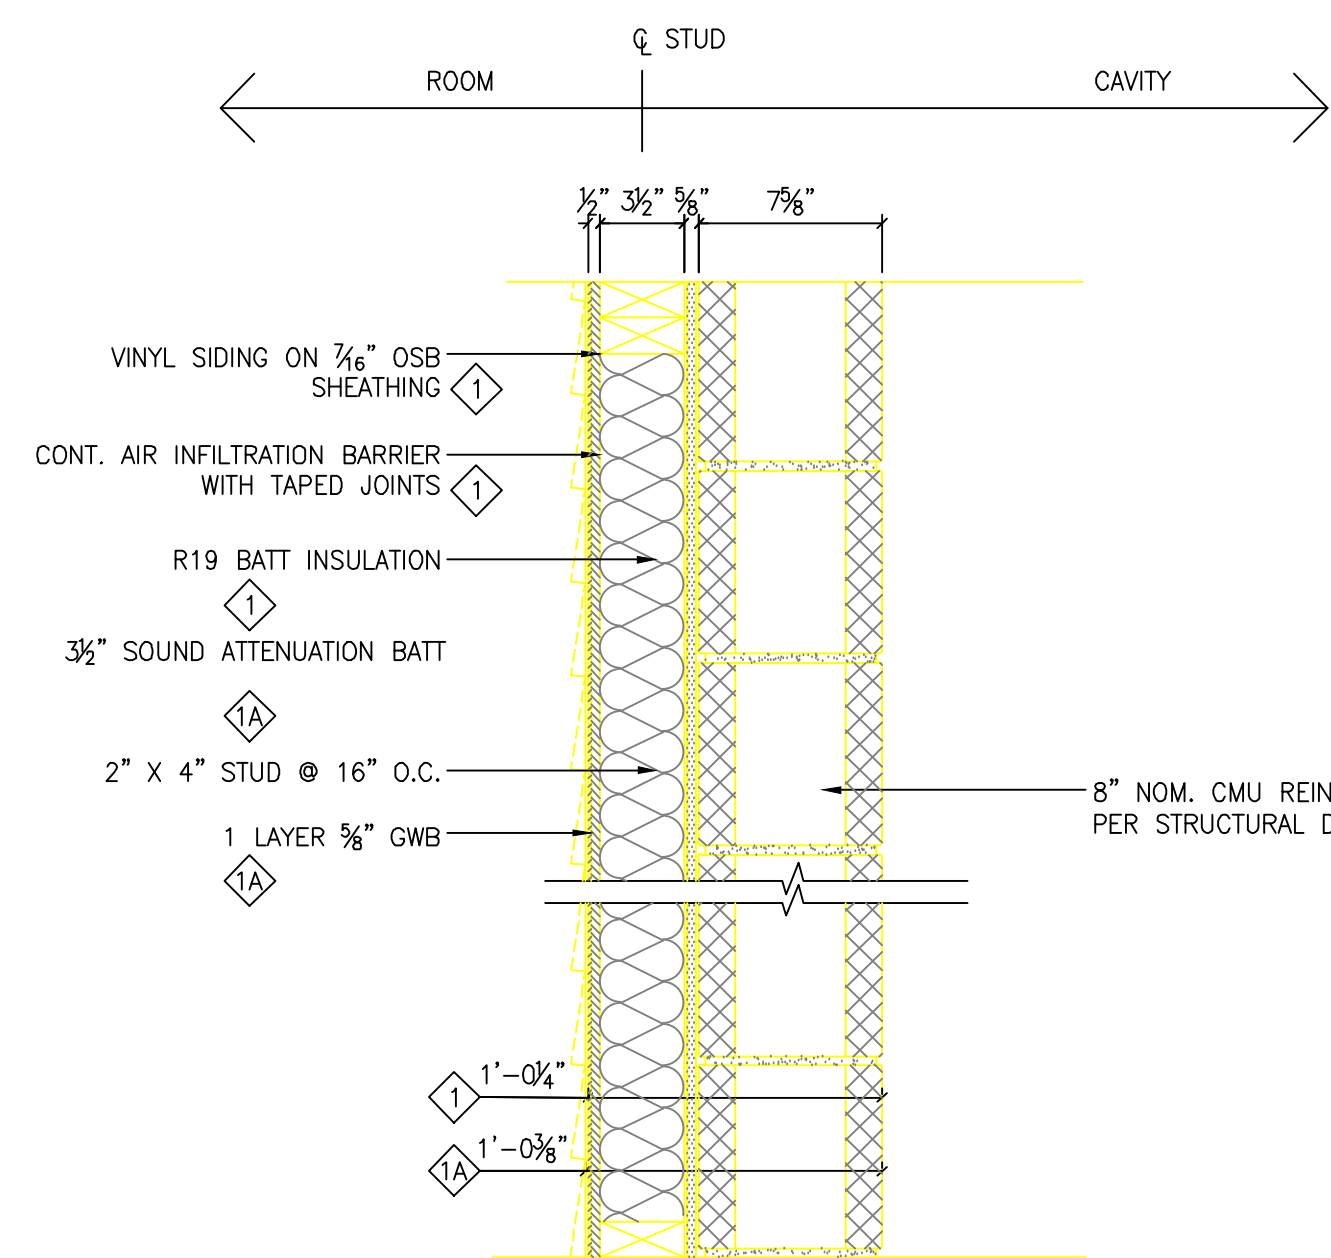

1 TWO HOUR RATED EXTERIOR BEARING FIRE WALL
SCALE: 1/8"=1'-0"
DESIGN NO. U306 (SIMILAR)
VINYL SIDING, 3/8" OSB SHEATHING, 2" X 4" WOOD FRAME WITH 3/8" SOUND BATT INS., AIR INFILTRATION BARRIER ON EXTERIOR SIDE, 8" NOM. CMU.
1 LAYER 3/8" FIRE RATED GWB ON 3/4" FURRING CHANNELS ON STAIR SIDE.

1A TWO HOUR RATED EXTERIOR BEARING FIRE WALL
SCALE: 1/8"=1'-0"
DESIGN NO. U306 (SIMILAR)
1 LAYER 3/8" FIRE RATED GWB, 2" X 4" WOOD FRAME WITH 3/8" SOUND ATTENUATION BATT ON ROOM SIDE.
1 LAYER DENSGLASS GOLD OR EQUAL, 8" NOM. CMU.

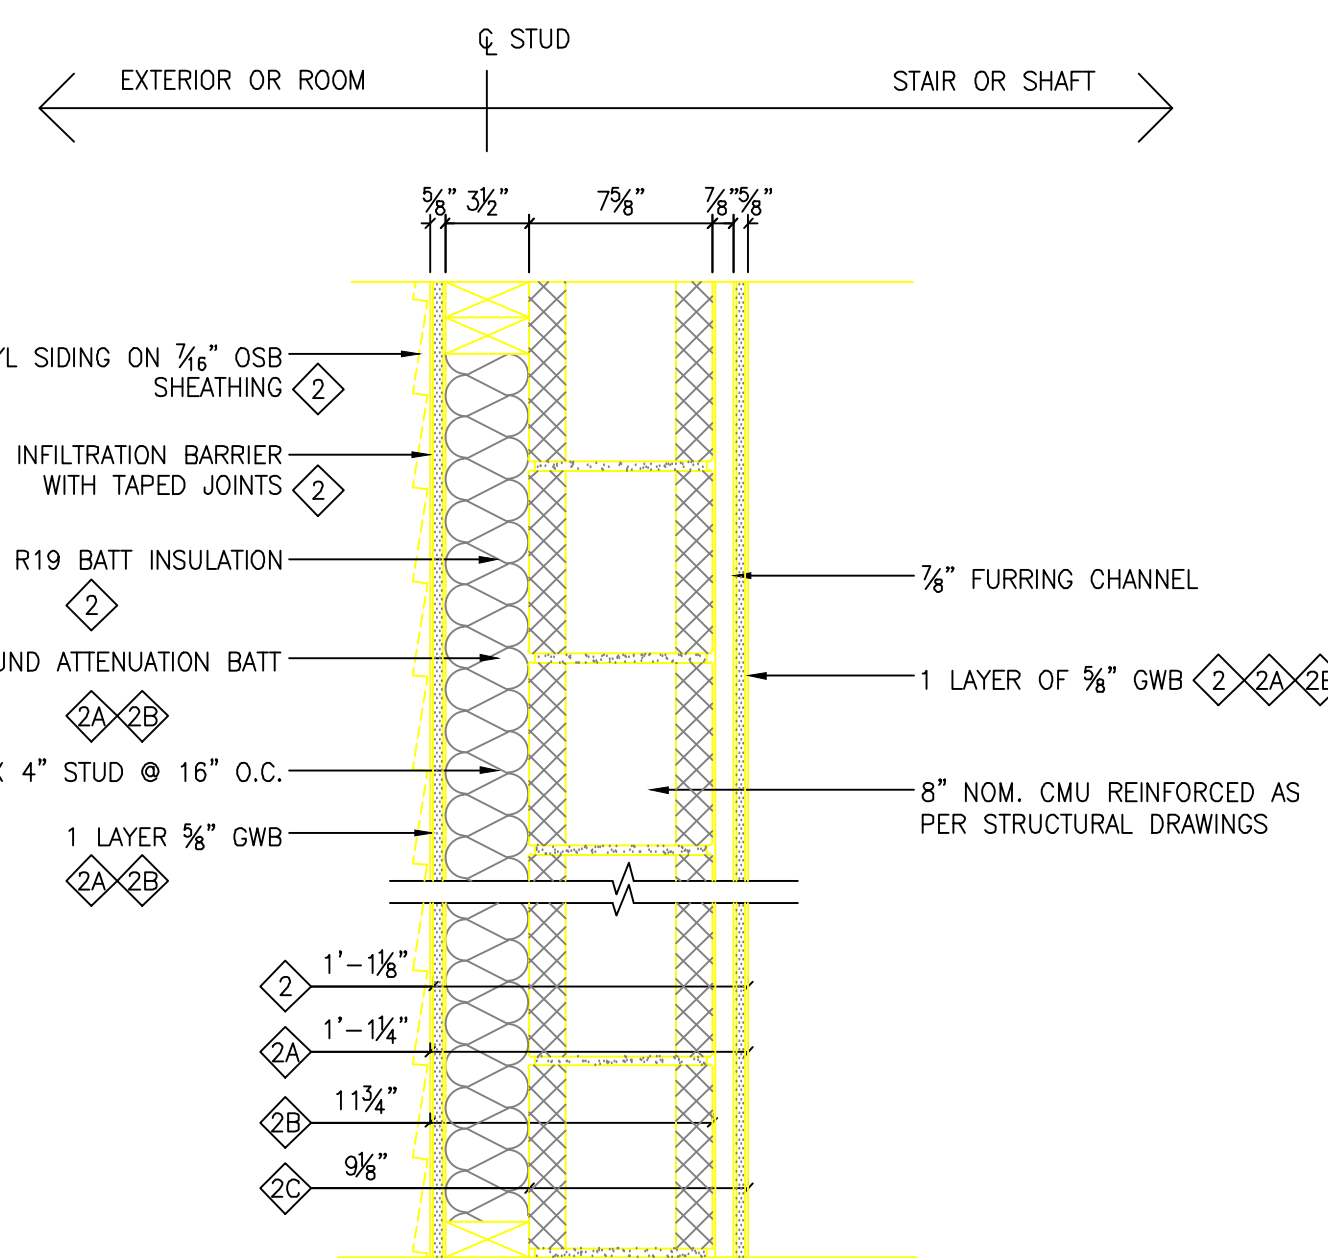


2 ONE HOUR RATED EXTERIOR MASONRY PARTITION
SCALE: 1/8"=1'-0"
DESIGN NO. U306 (SIMILAR)
VINYL SIDING, 3/8" OSB SHEATHING, 2" X 4" WOOD FRAME WITH 3/8" SOUND BATT INS., AIR INFILTRATION BARRIER ON EXTERIOR SIDE, 8" NOM. CMU.
1 LAYER 3/8" FIRE RATED GWB ON 3/4" FURRING CHANNELS ON STAIR SIDE.

2A ONE HOUR RATED EXTERIOR MASONRY PARTITION
SCALE: 1/8"=1'-0"
DESIGN NO. U306 (SIMILAR)
1 LAYER 3/8" FIRE RATED GWB ON 2" X 4" WOOD FRAME WITH 3/8" SOUND ATTENUATION BATT ON ROOM SIDE.
8" NOM. CMU.
1 LAYER 3/8" FIRE RATED GWB ON 3/4" FURRING CHANNELS ON STAIR SIDE.


2B ONE HOUR RATED EXTERIOR MASONRY PARTITION
SCALE: 1/8"=1'-0"
DESIGN NO. U306 (SIMILAR)
1 LAYER 3/8" FIRE RATED GWB ON 2" X 4" WOOD FRAME WITH 3/8" SOUND ATTENUATION BATT ON ROOM SIDE.
8" NOM. CMU.
NO FURRING OR GWB ON SHAFT SIDE.

2C ONE HOUR RATED INTERIOR MASONRY PARTITION
SCALE: 1/8"=1'-0"
DESIGN NO. U306 (SIMILAR)
NO GWB, WOOD FRAME OR SOUND ATTENUATION BATT ON ROOM SIDE.
8" NOM. CMU.
1 LAYER 3/8" FIRE RATED GWB ON 3/4" FURRING CHANNELS ON STAIR SIDE.

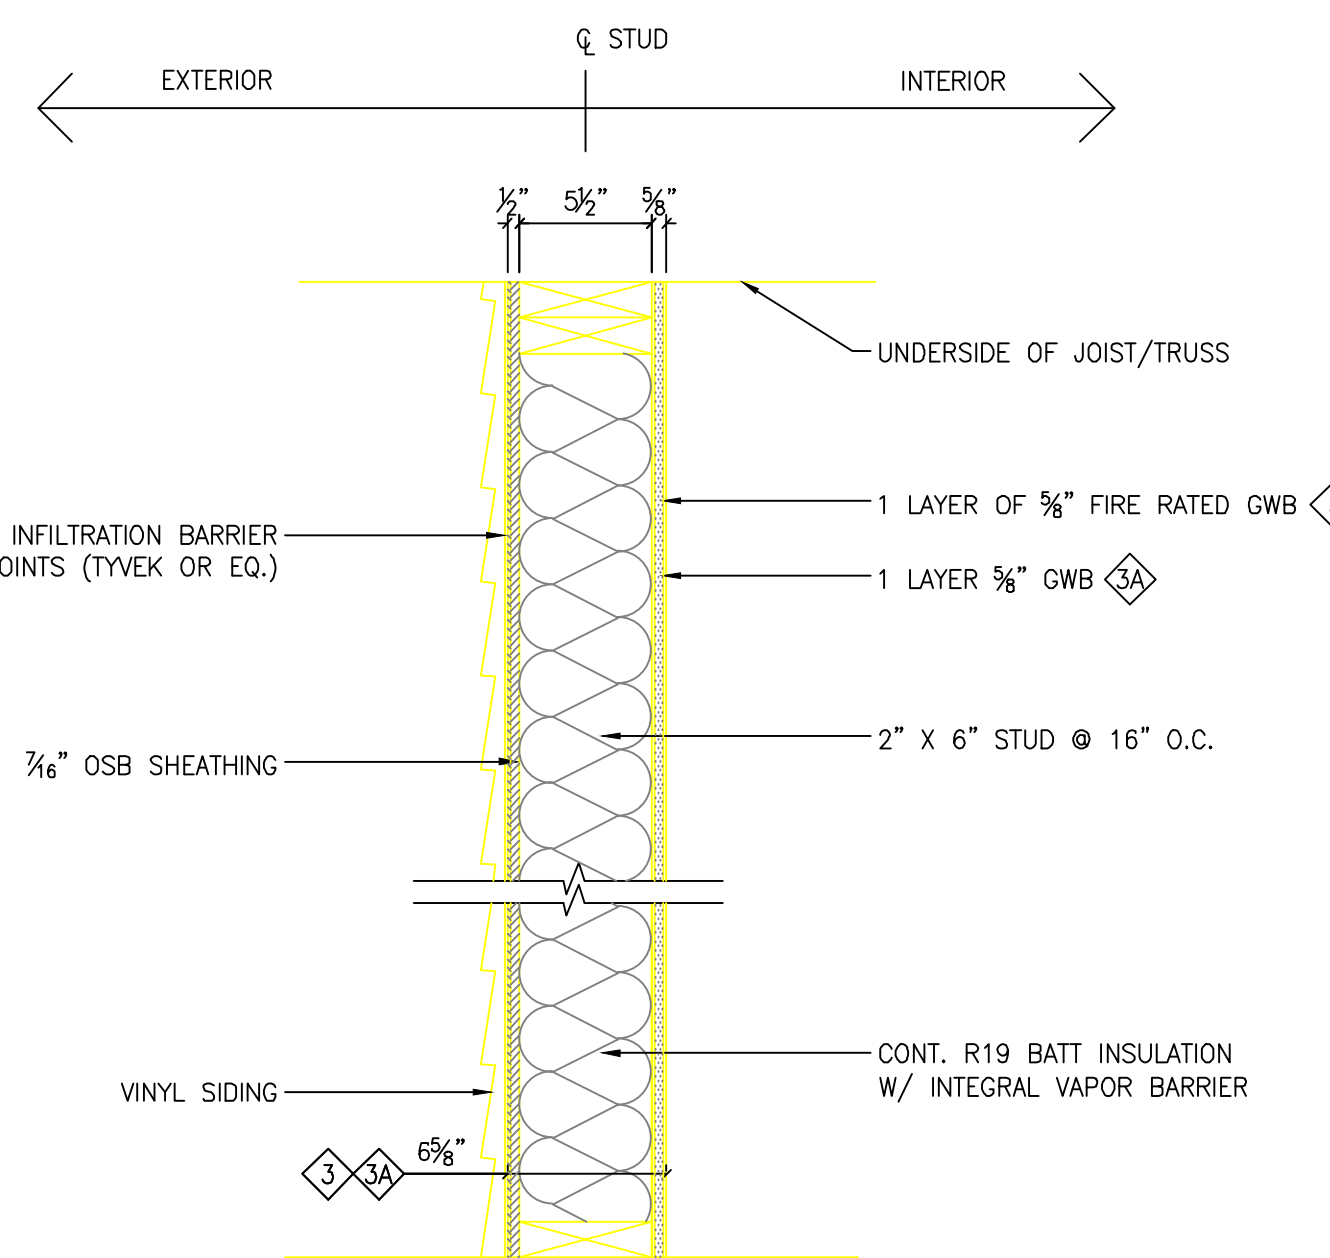


3 ONE HOUR RATED EXTERIOR BEARING PARTITION
SCALE: 1/8"=1'-0"
DESIGN NO. U306 (SIMILAR)
VINYL SIDING, 1 LAYER 3/8" OSB SHEATHING WITH AIR INFILTRATION BARRIER ON EXTERIOR SIDE.
2" X 6" WOOD FRAME WITH R19 BATT INSULATION.
1 LAYER 3/8" FIRE RATED GWB ON INTERIOR SIDE.

3A NON-RATED EXTERIOR BEARING PARTITION
SCALE: 1/8"=1'-0"
DESIGN NO. U306 (SIMILAR)
VINYL SIDING, 1 LAYER 3/8" OSB SHEATHING WITH AIR INFILTRATION BARRIER ON EXTERIOR SIDE.
2" X 6" WOOD FRAME WITH R19 BATT INSULATION.
1 LAYER 3/8" GWB ON INTERIOR SIDE.

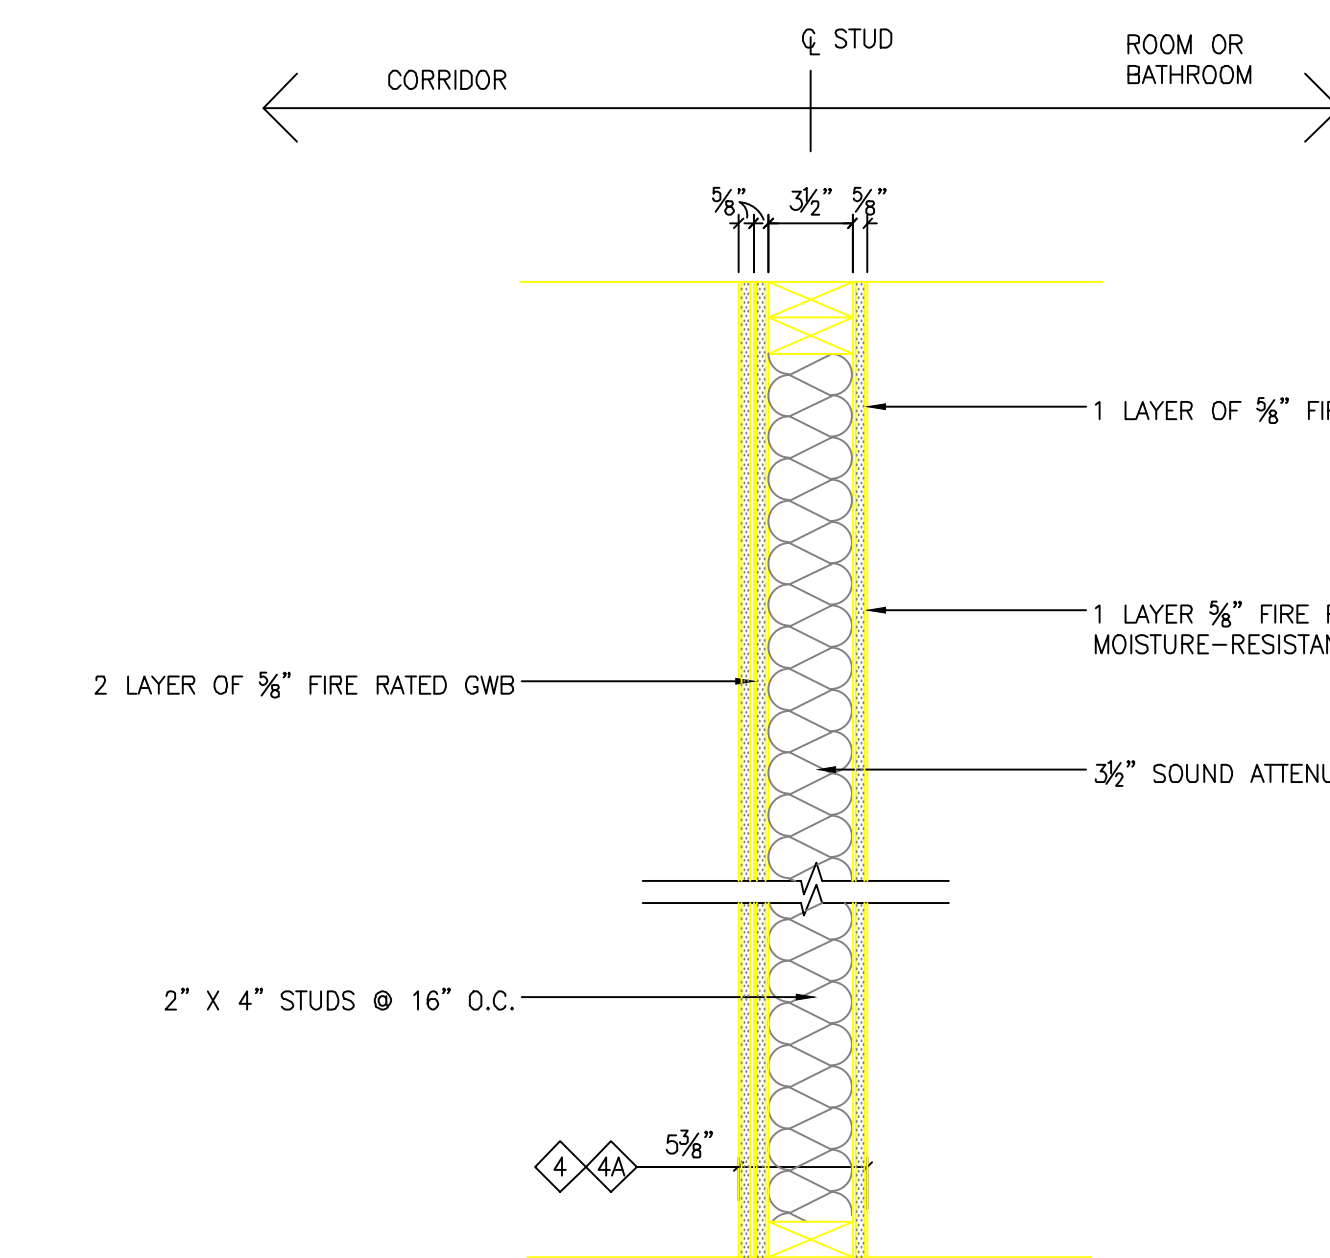

4 ONE HR RATED INTERIOR BEARING PARTITION
SCALE: 1/8"=1'-0"
DESIGN NO. U306 (SIMILAR)
2 LAYER 3/8" FIRE RATED GWB ON CORRIDOR SIDE.
2" X 4" WOOD FRAME WITH 3/8" SOUND ATTENUATION BATT.
1 LAYER 3/8" FIRE RATED GWB ON ROOM SIDE.

4A ONE HR RATED INTERIOR BEARING PARTITION
SCALE: 1/8"=1'-0"
DESIGN NO. U306 (SIMILAR)
2 LAYER 3/8" FIRE RATED GWB ON CORRIDOR SIDE.
2" X 4" WOOD FRAME WITH 3/8" SOUND ATTENUATION BATT.
1 LAYER 3/8" FIRE RATED MOISTURE-RESISTANT GWB ON BATHROOM SIDE.

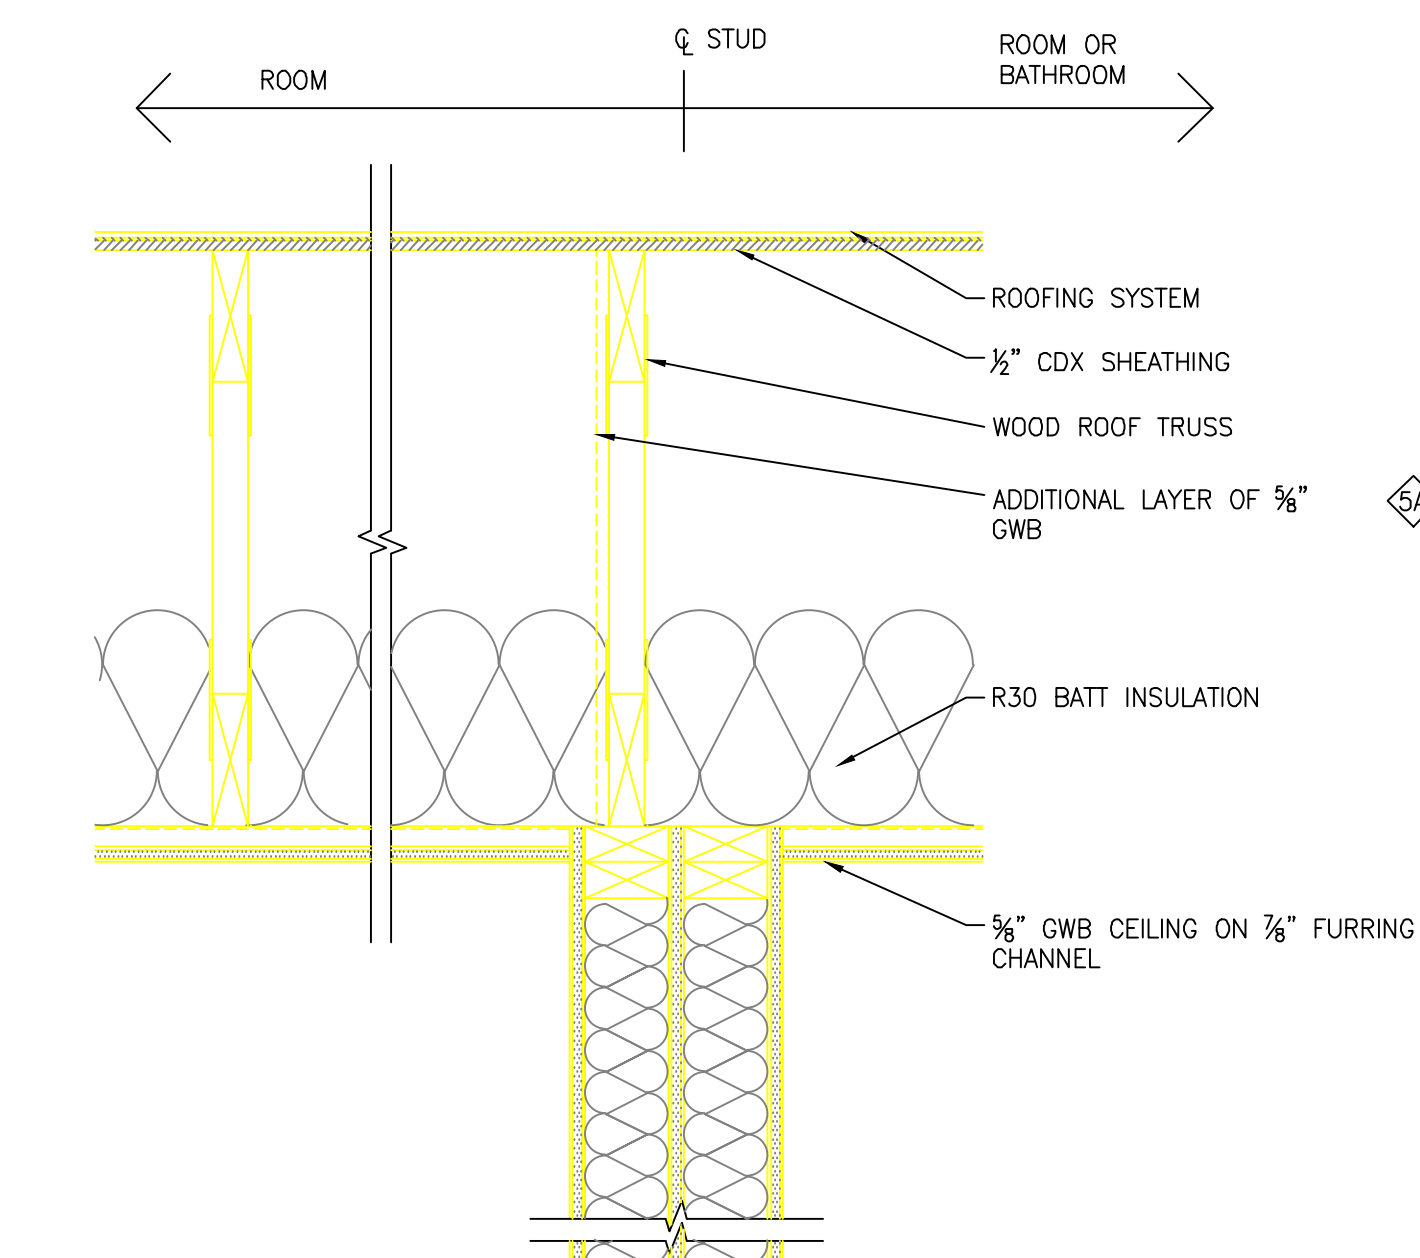


5 ONE HOUR RATED INTERIOR DEMISING PARTITION
SCALE: 1/8"=1'-0"
DESIGN NO. U306 (SIMILAR)
1 LAYER 3/8" FIRE RATED GWB, 2" X 4" WOOD FRAME WITH 3/8" SOUND ATTENUATION BATT ON ROOM SIDE.
1 LAYER 3/8" DENSGLASS GOLD OR EQUAL.
1 LAYER 3/8" FIRE RATED GWB, 2" X 4" WOOD FRAME WITH 3/8" SOUND ATTENUATION BATT ON OTHER SIDE.

5A ONE HOUR RATED INTERIOR DEMISING PARTITION
SCALE: 1/8"=1'-0"
DESIGN NO. U306 (SIMILAR)
1 LAYER 3/8" FIRE RATED GWB, 2" X 4" WOOD FRAME WITH 3/8" SOUND ATTENUATION BATT ON ROOM SIDE.
1 LAYER 3/8" DENSGLASS GOLD OR EQUAL.
1 LAYER 3/8" FIRE RATED GWB, 2" X 4" WOOD FRAME WITH 3/8" SOUND ATTENUATION BATT ON OTHER SIDE.

5B ONE HOUR RATED INTERIOR DEMISING PARTITION
SCALE: 1/8"=1'-0"
DESIGN NO. U306 (SIMILAR)
1 LAYER 3/8" FIRE RATED GWB, 2" X 4" WOOD FRAME WITH 3/8" SOUND ATTENUATION BATT ON ROOM SIDE.
1 LAYER 3/8" DENSGLASS GOLD OR EQUAL.
1 LAYER 3/8" FIRE RATED MOISTURE-RESISTANT GWB, 2" X 4" WOOD FRAME WITH 3/8" SOUND ATTENUATION BATT ON BATHROOM SIDE.

5C ONE HOUR RATED INTERIOR DEMISING PARTITION
SCALE: 1/8"=1'-0"
DESIGN NO. U306 (SIMILAR)
1 LAYER 3/8" FIRE RATED GWB, 2" X 4" WOOD FRAME WITH 3/8" SOUND ATTENUATION BATT ON ROOM SIDE.
1 LAYER 3/8" DENSGLASS GOLD OR EQUAL.
1 LAYER 3/8" FIRE RATED MOISTURE-RESISTANT GWB, 2" X 4" WOOD FRAME WITH 3/8" SOUND ATTENUATION BATT ON BATHROOM SIDE.
1 ADDITIONAL LAYER 3/8" MOISTURE-RESISTANT GWB TO COVER EDGE OF TUB.

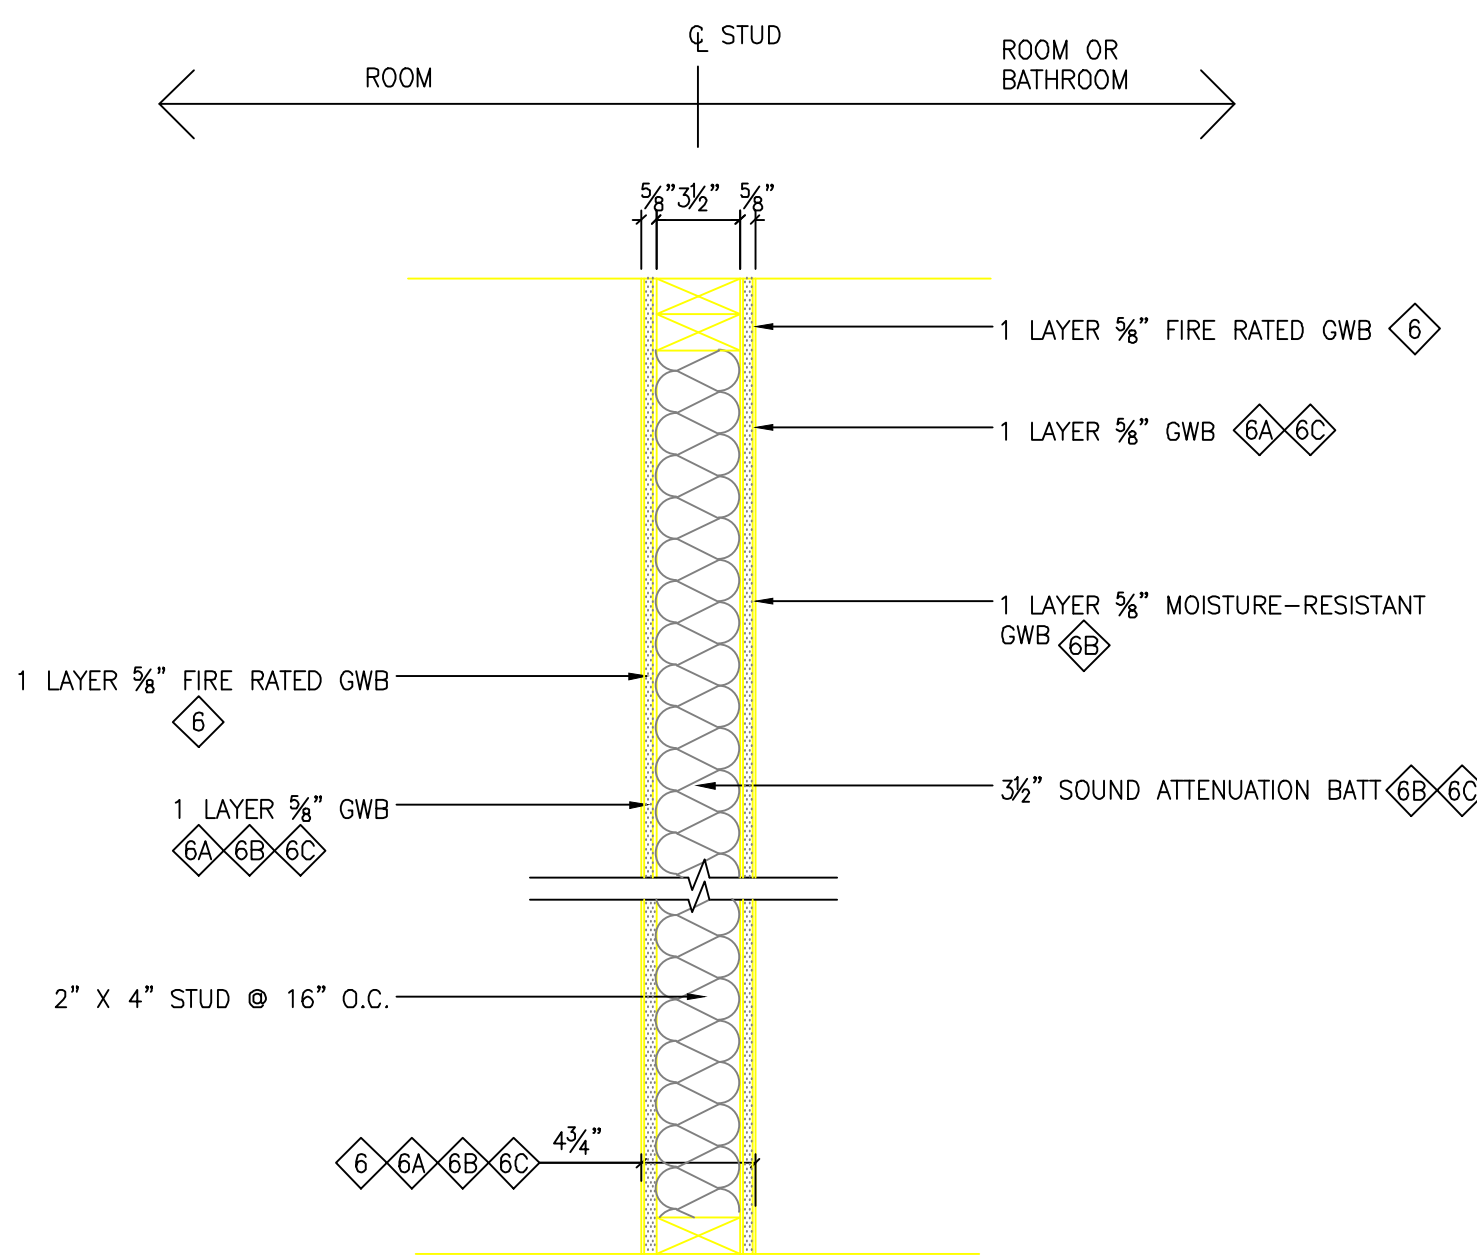


6 ONE HR RATED INTERIOR BEARING PARTITION
SCALE: 1/8"=1'-0"
DESIGN NO. U306 (SIMILAR)
1 LAYER 3/8" FIRE RATED GWB ON EACH SIDE.
2" X 4" WOOD FRAME WITH 3/8" SOUND ATTENUATION BATT.

6A NON-RATED INTERIOR PARTITION
SCALE: 1/8"=1'-0"
DESIGN NO. U306 (SIMILAR)
1 LAYER 3/8" GWB ON EACH SIDE.
2" X 4" WOOD FRAME


6B NON-RATED INTERIOR PARTITION
SCALE: 1/8"=1'-0"
DESIGN NO. U306 (SIMILAR)
1 LAYER 3/8" GWB ON ROOM SIDE.
2" X 4" WOOD FRAME WITH 3/8" SOUND ATTENUATION BATT.
1 LAYER 3/8" MOISTURE-RESISTANT GWB ON BATHROOM SIDE.

6C NON-RATED INTERIOR PARTITION
SCALE: 1/8"=1'-0"
DESIGN NO. U306 (SIMILAR)
1 LAYER 3/8" GWB ON EACH SIDE.
2" X 4" WOOD FRAME WITH 3/8" SOUND ATTENUATION BATT.

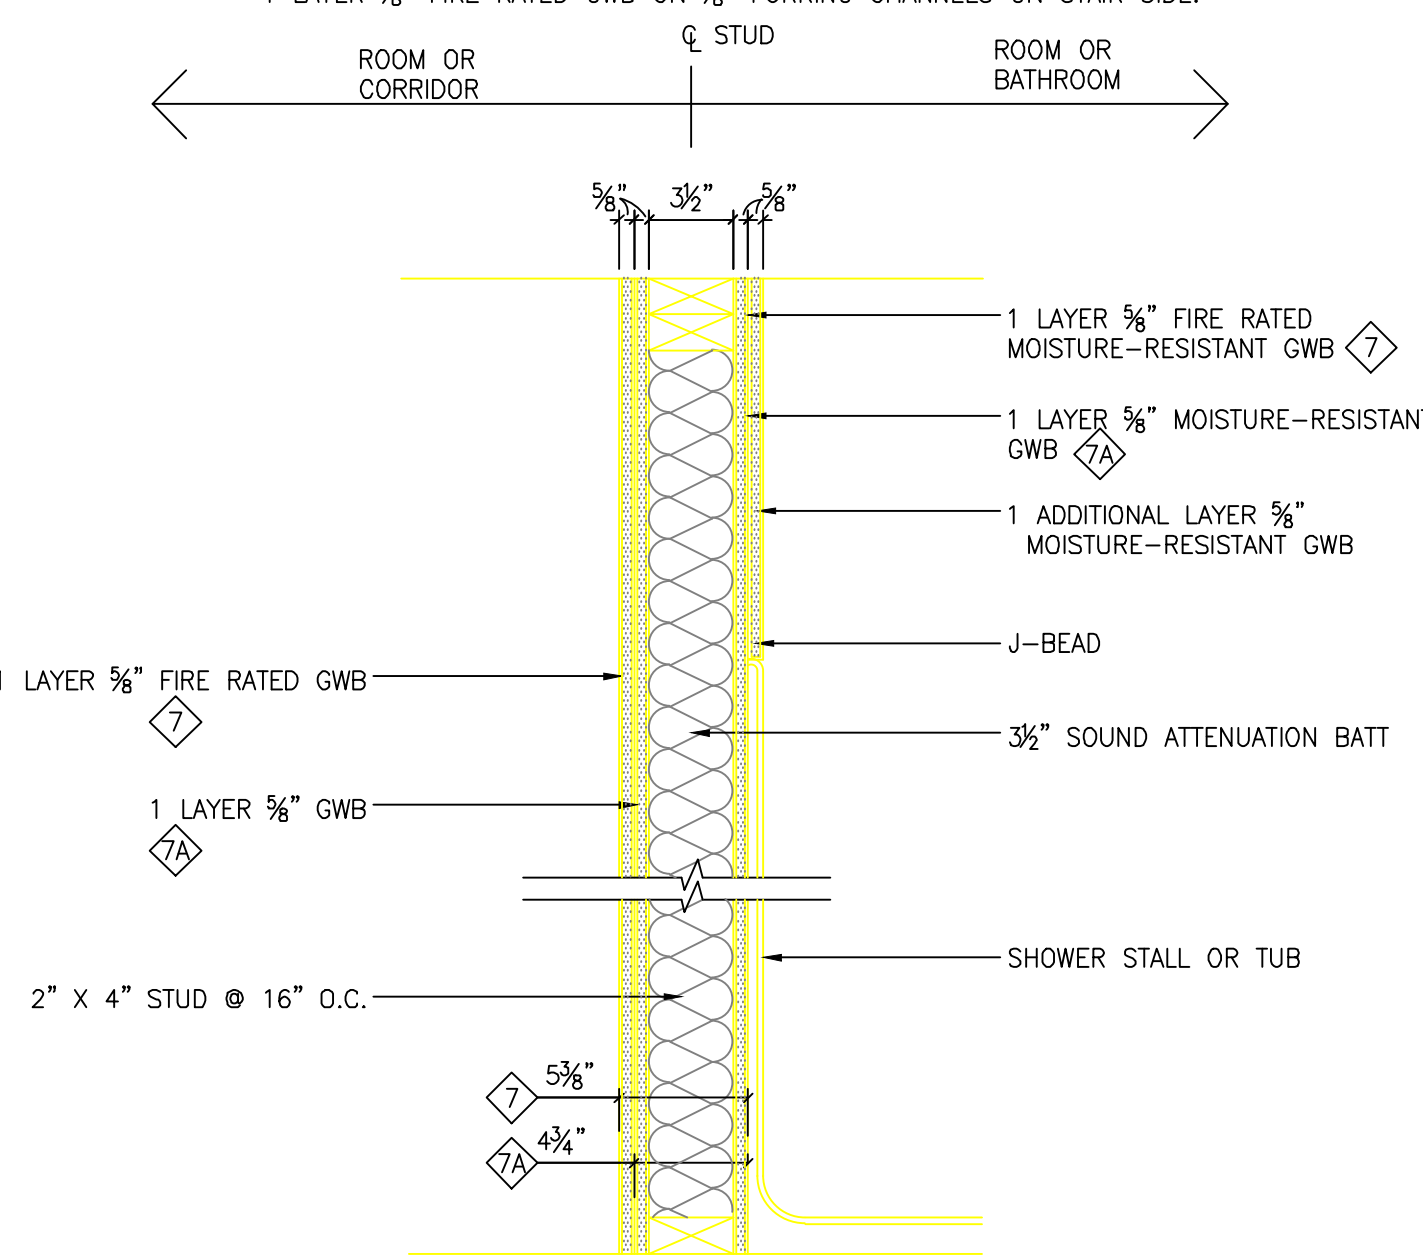


7 ONE HR RATED INTERIOR BEARING PARTITION
SCALE: 1/8"=1'-0"
DESIGN NO. U306 (SIMILAR)
2 LAYERS 3/8" FIRE RATED GWB ON CORRIDOR SIDE.
2" X 4" WOOD FRAME WITH 3/8" SOUND ATTENUATION BATT.
1 LAYER 3/8" FIRE RATED MOISTURE-RESISTANT GWB ON BATHROOM SIDE.
1 ADDITIONAL LAYER 3/8" MOISTURE-RESISTANT GWB TO COVER EDGE OF TUB.

7A NON-RATED INTERIOR PARTITION
SCALE: 1/8"=1'-0"
DESIGN NO. U306 (SIMILAR)
1 LAYER 3/8" GWB ON ROOM SIDE.
2" X 4" WOOD FRAME WITH 3/8" SOUND ATTENUATION BATT.
1 LAYER 3/8" MOISTURE-RESISTANT GWB ON BATHROOM SIDE.
1 ADDITIONAL LAYER 3/8" MOISTURE-RESISTANT GWB TO COVER EDGE OF TUB.

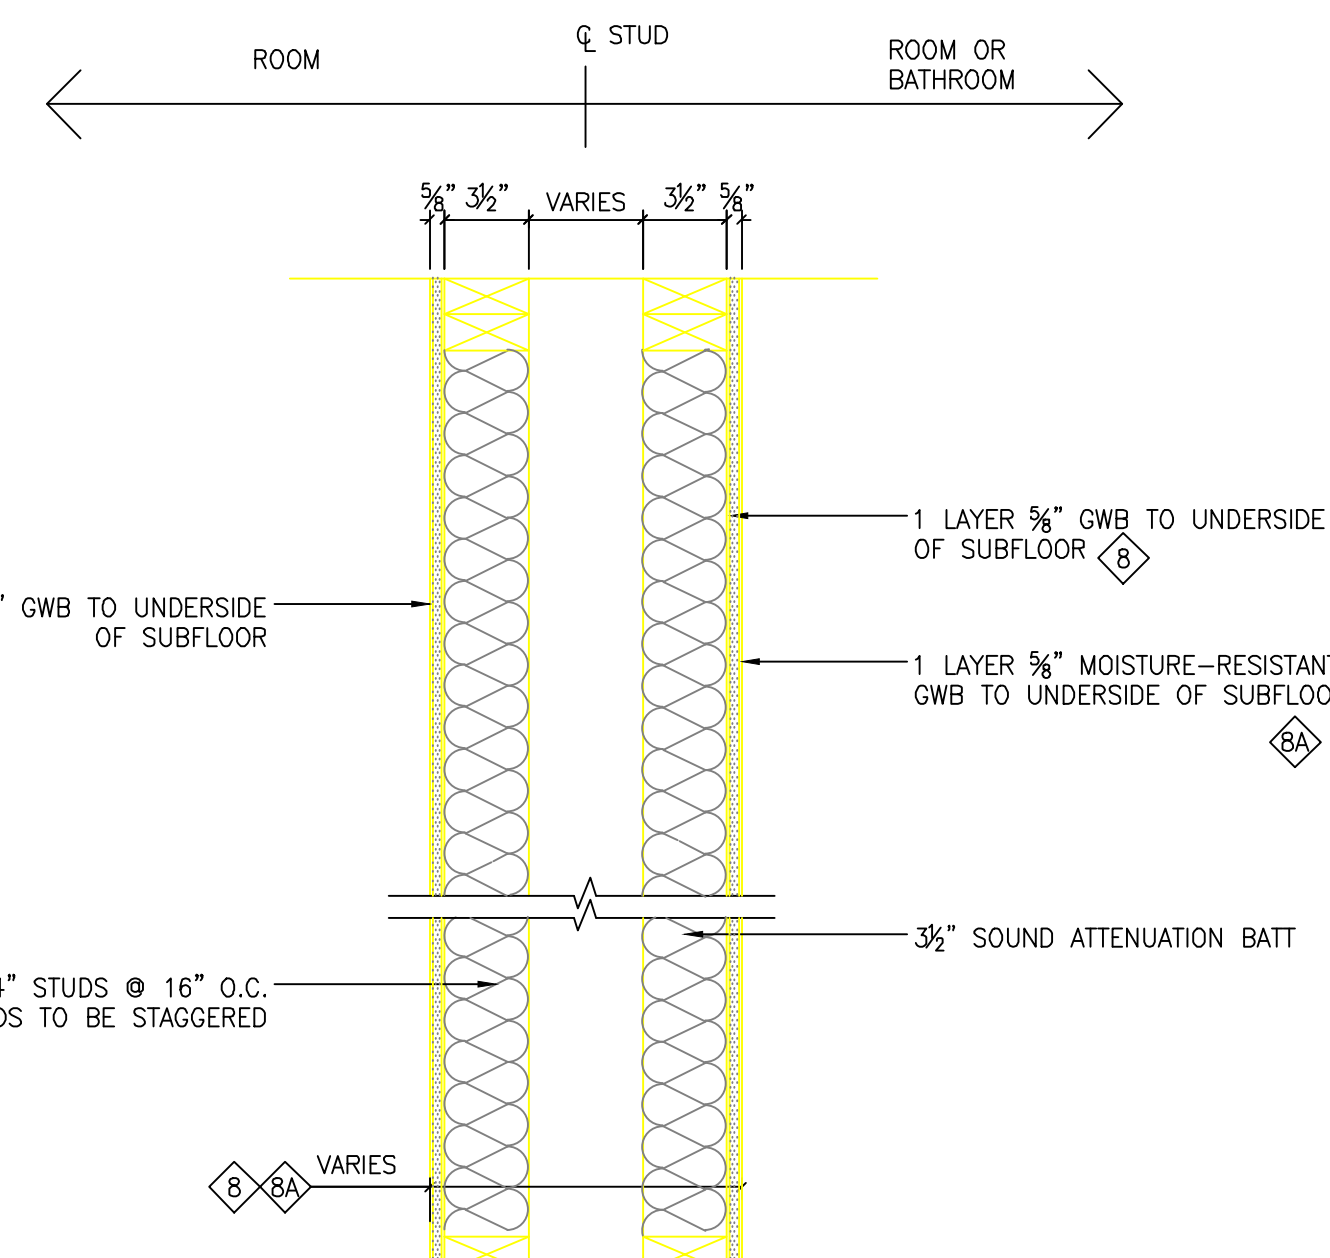


8 NON-RATED PLUMBING CHASE
SCALE: 1/8"=1'-0"
DESIGN NO. U306 (SIMILAR)
1 LAYER 3/8" GWB, 2" X 4" WOOD FRAME WITH 3/8" SOUND ATTENUATION BATT ON ROOM SIDE.
1 LAYER 3/8" GWB, 2" X 4" WOOD FRAME WITH 3/8" SOUND ATTENUATION BATT ON OTHER SIDE.

8A NON-RATED PLUMBING CHASE
SCALE: 1/8"=1'-0"
DESIGN NO. U306 (SIMILAR)
1 LAYER 3/8" GWB, 2" X 4" WOOD FRAME WITH 3/8" SOUND ATTENUATION BATT ON ROOM SIDE.
1 LAYER 3/8" MOISTURE-RESISTANT GWB, 2" X 4" WOOD FRAME WITH 3/8" SOUND ATTENUATION BATT ON BATHROOM SIDE.

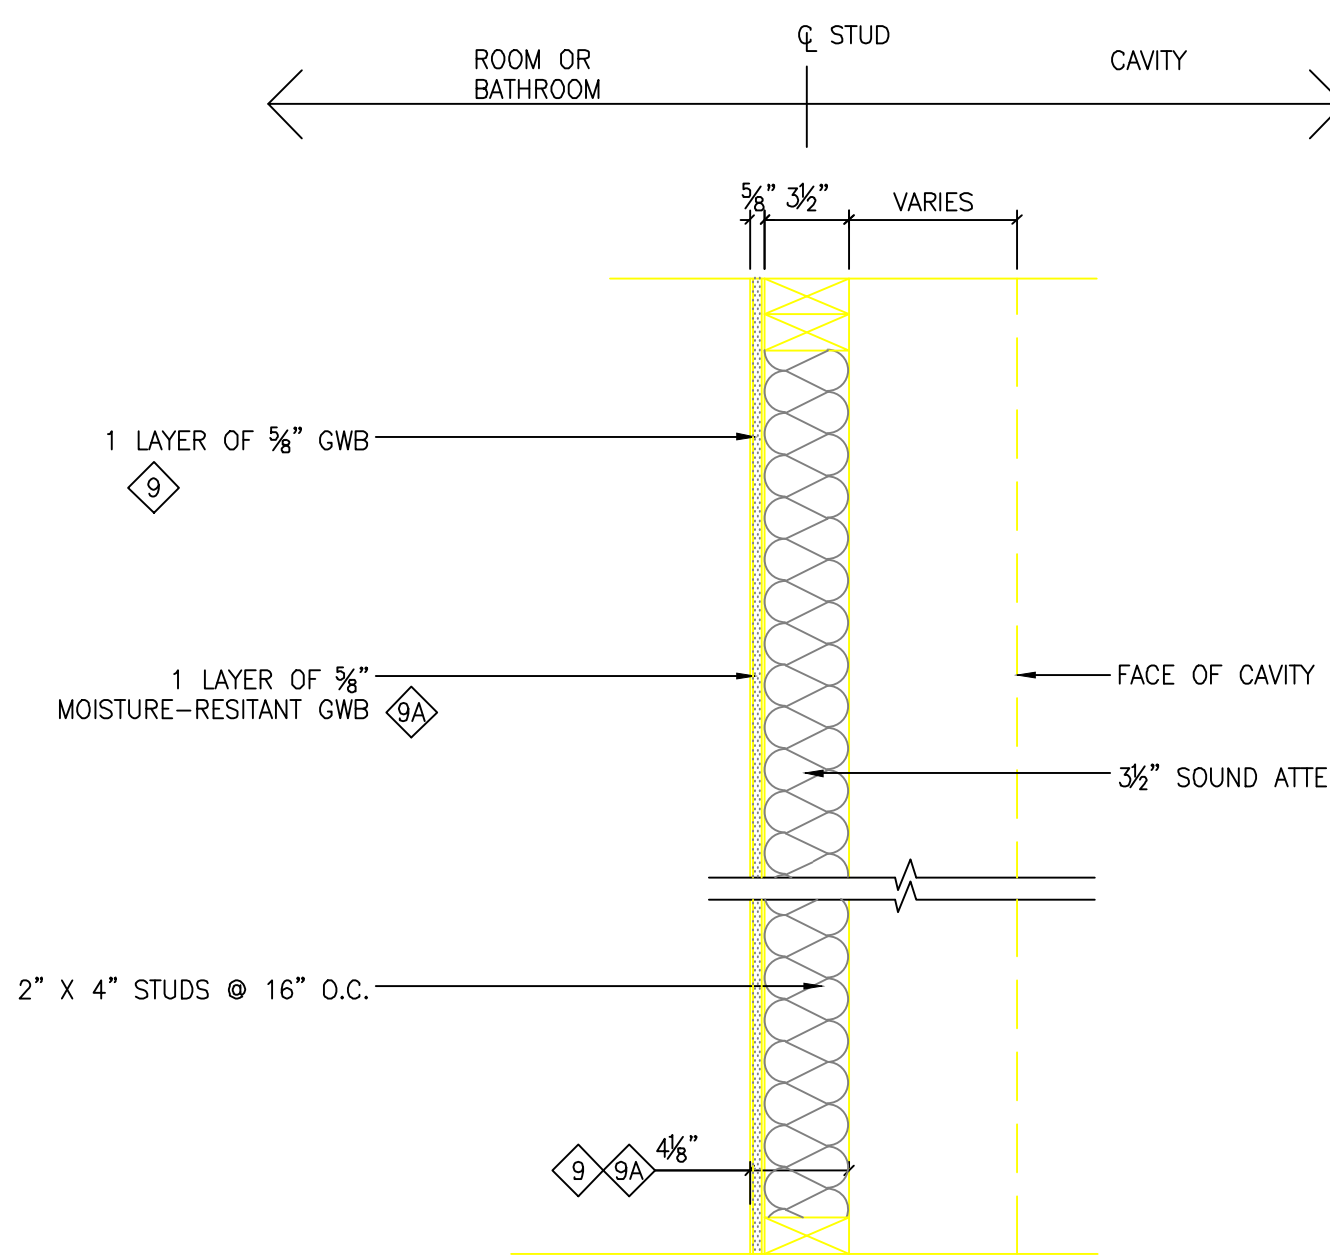


9 NON-RATED INTERIOR FURRING
SCALE: 1/8"=1'-0"
DESIGN NO. U306 (SIMILAR)
1 LAYER 3/8" GWB ON ROOM SIDE.
2" X 4" WOOD FRAME WITH 3/8" SOUND ATTENUATION BATT.

9A NON-RATED INTERIOR FURRING
SCALE: 1/8"=1'-0"
DESIGN NO. U306 (SIMILAR)
1 LAYER 3/8" MOISTURE-RESISTANT GWB ON BATHROOM SIDE.
2" X 4" WOOD FRAME WITH 3/8" SOUND ATTENUATION BATT.

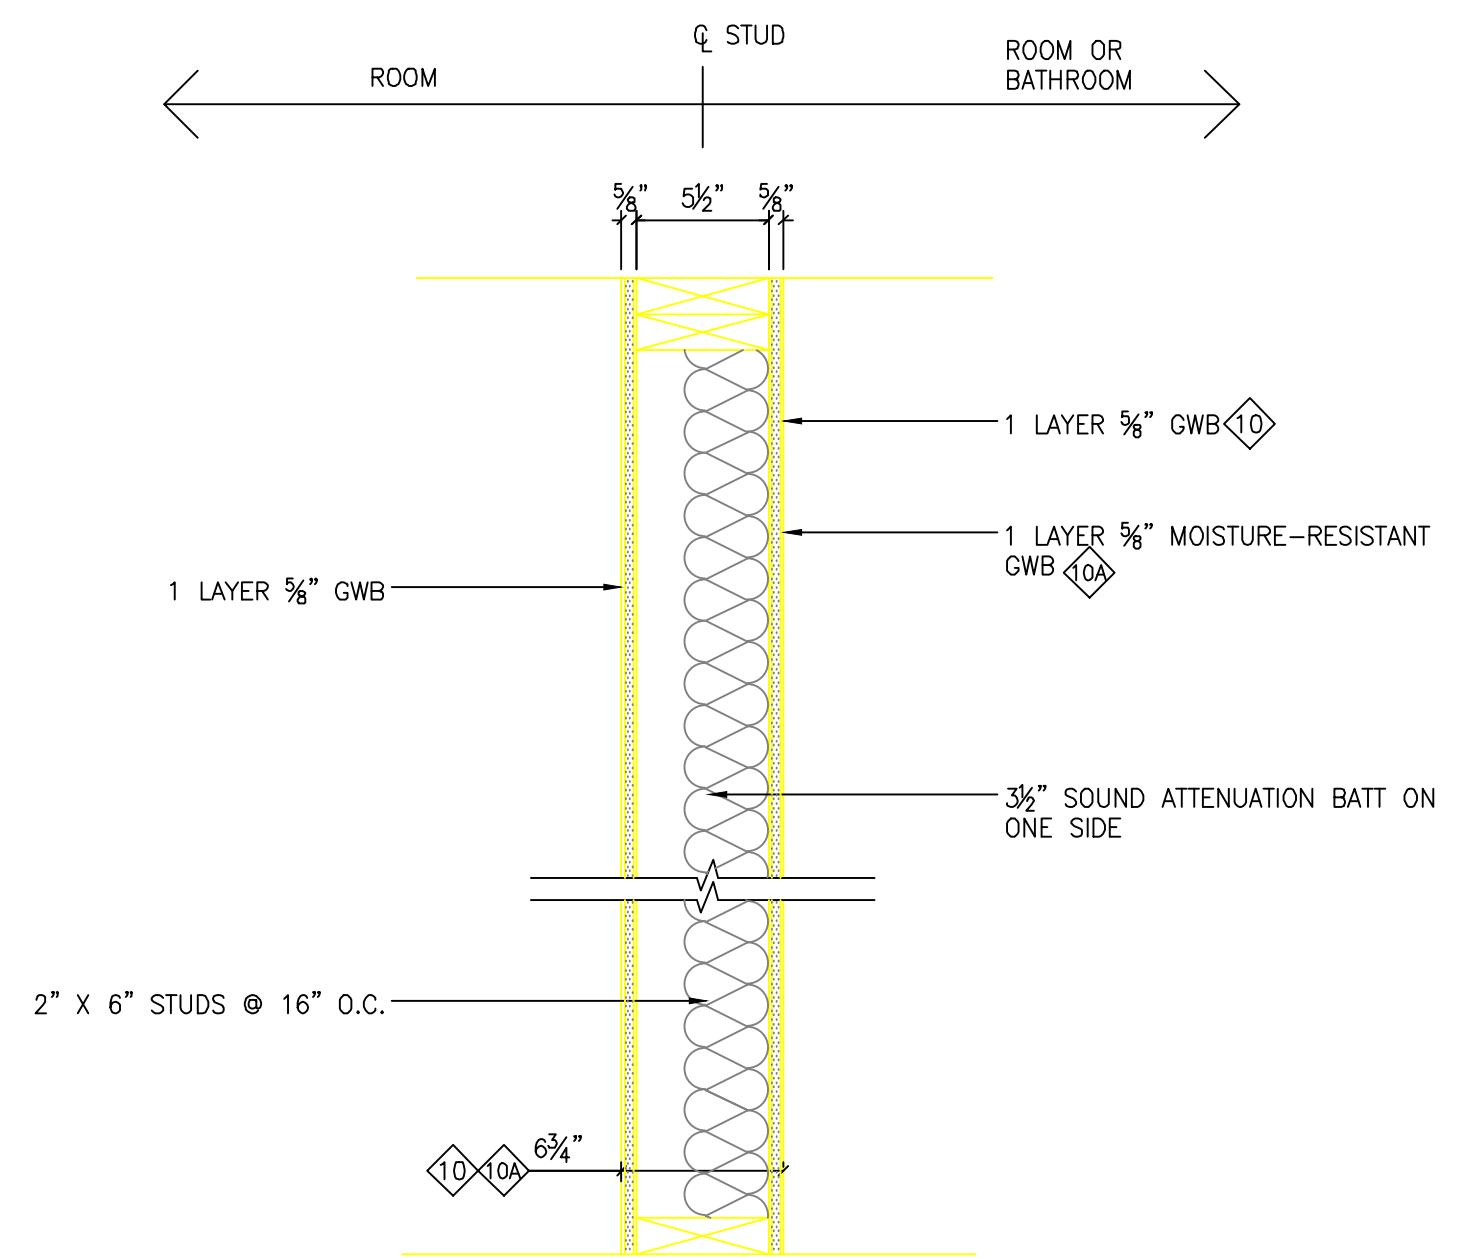


10 NON-RATED INTERIOR PARTITION
SCALE: 1/8"=1'-0"
DESIGN NO. U306 (SIMILAR)
1 LAYER 3/8" GWB ON EACH SIDE.
2" X 6" WOOD FRAME WITH 3/8" SOUND ATTENUATION BATT.


10A NON-RATED INTERIOR PARTITION
SCALE: 1/8"=1'-0"
DESIGN NO. U306 (SIMILAR)
1 LAYER 3/8" GWB ON ROOM SIDE.
2" X 6" WOOD FRAME WITH 3/8" SOUND ATTENUATION BATT.
1 LAYER 3/8" MOISTURE-RESISTANT GWB ON BATHROOM SIDE.

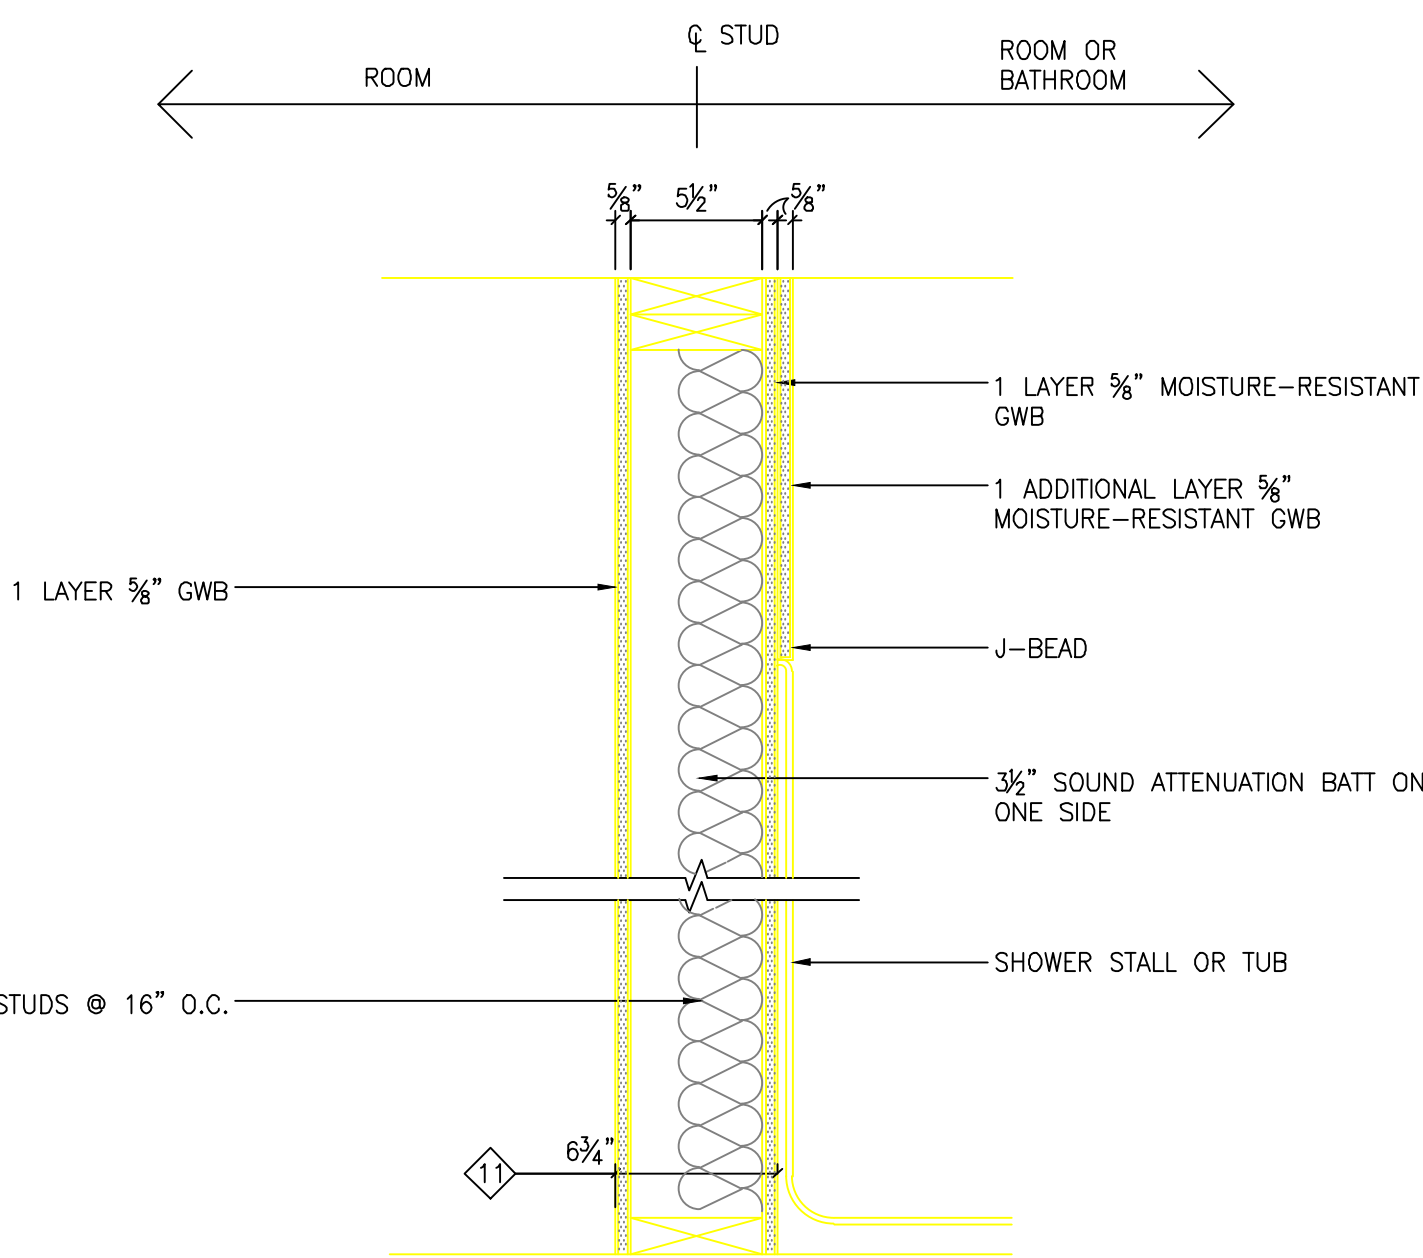

11 NON-RATED INTERIOR PARTITION
SCALE: 1/8"=1'-0"
DESIGN NO. U306 (SIMILAR)
1 LAYER 3/8" GWB ON ROOM SIDE.
2" X 6" WOOD FRAME WITH 3/8" SOUND ATTENUATION BATT.
1 LAYER 3/8" MOISTURE-RESISTANT GWB ON BATHROOM SIDE.
1 ADDITIONAL LAYER 3/8" MOISTURE-RESISTANT GWB TO COVER EDGE OF TUB.

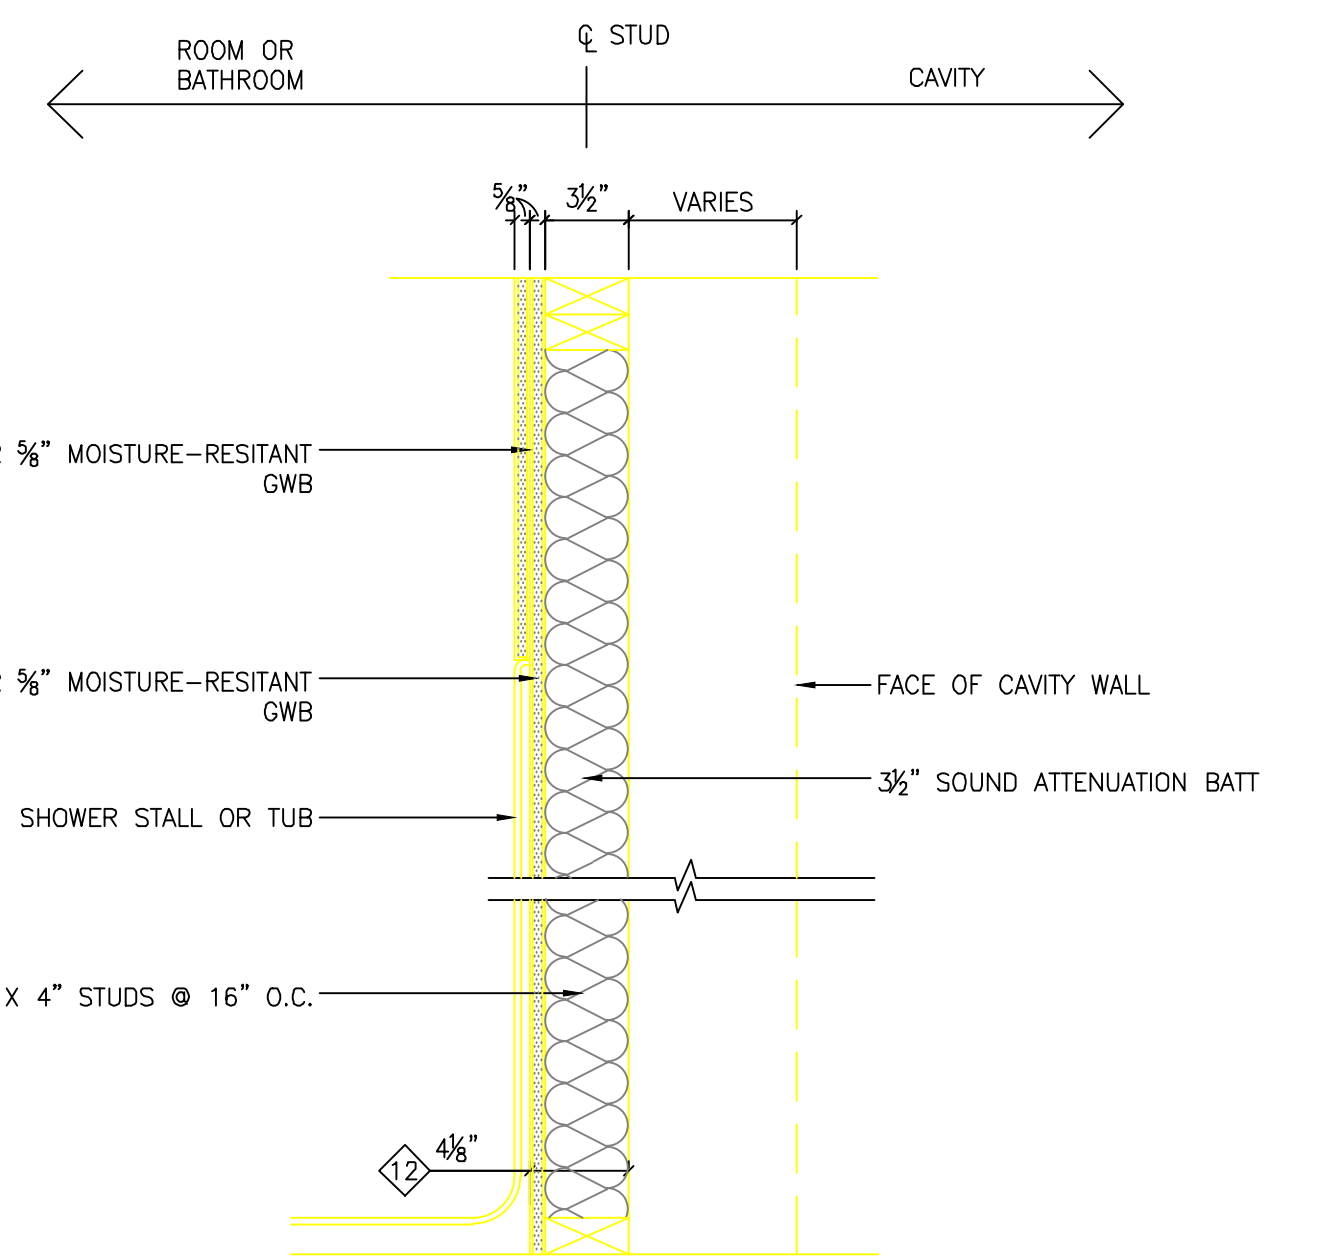

12 NON-RATED INTERIOR FURRING
SCALE: 1/8"=1'-0"
DESIGN NO. U306 (SIMILAR)
1 LAYER 3/8" MOISTURE-RESISTANT GWB ON BATHROOM SIDE.
1 ADDITIONAL LAYER 3/8" MOISTURE-RESISTANT GWB TO COVER EDGE OF TUB.
2" X 4" WOOD FRAME WITH 3/8" SOUND ATTENUATION BATT.

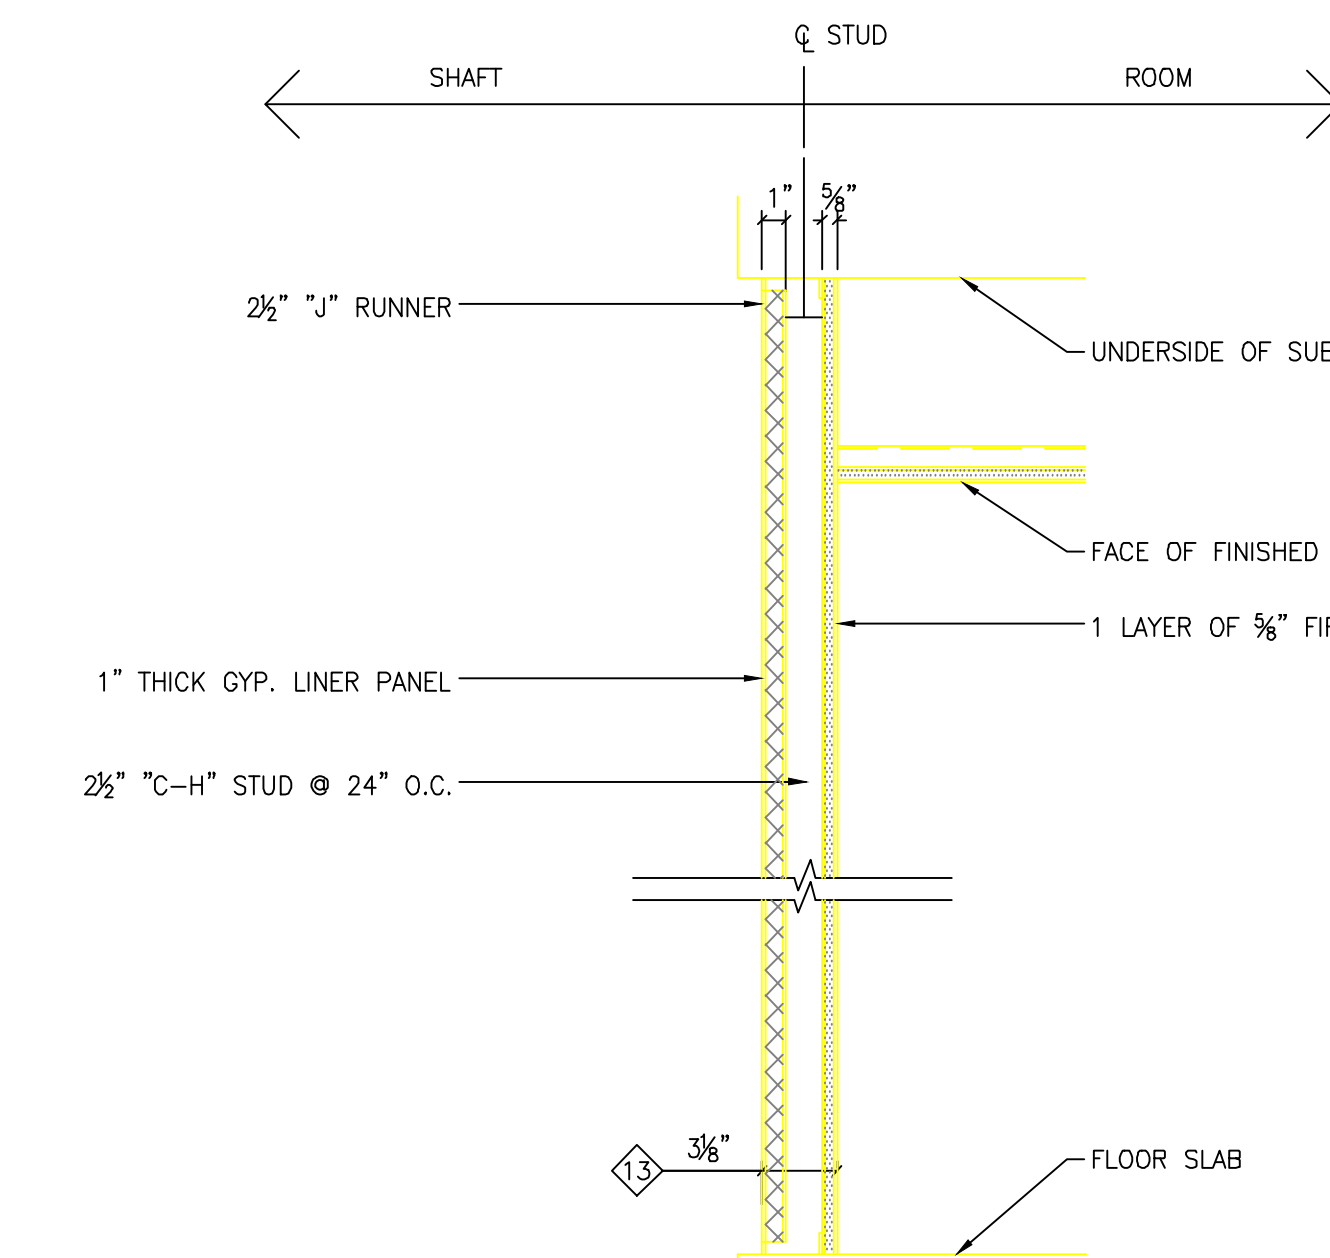

13 ONE HR RATED SHAFT WALL
SCALE: 1/8"=1'-0"
DESIGN NO. U469
1" THICK GYP. LINER PANEL ON SHAFT SIDE.
2x4" C-H" STUD @ 24" O.C.
1 LAYER 3/8" GWB ON ROOM SIDE.